


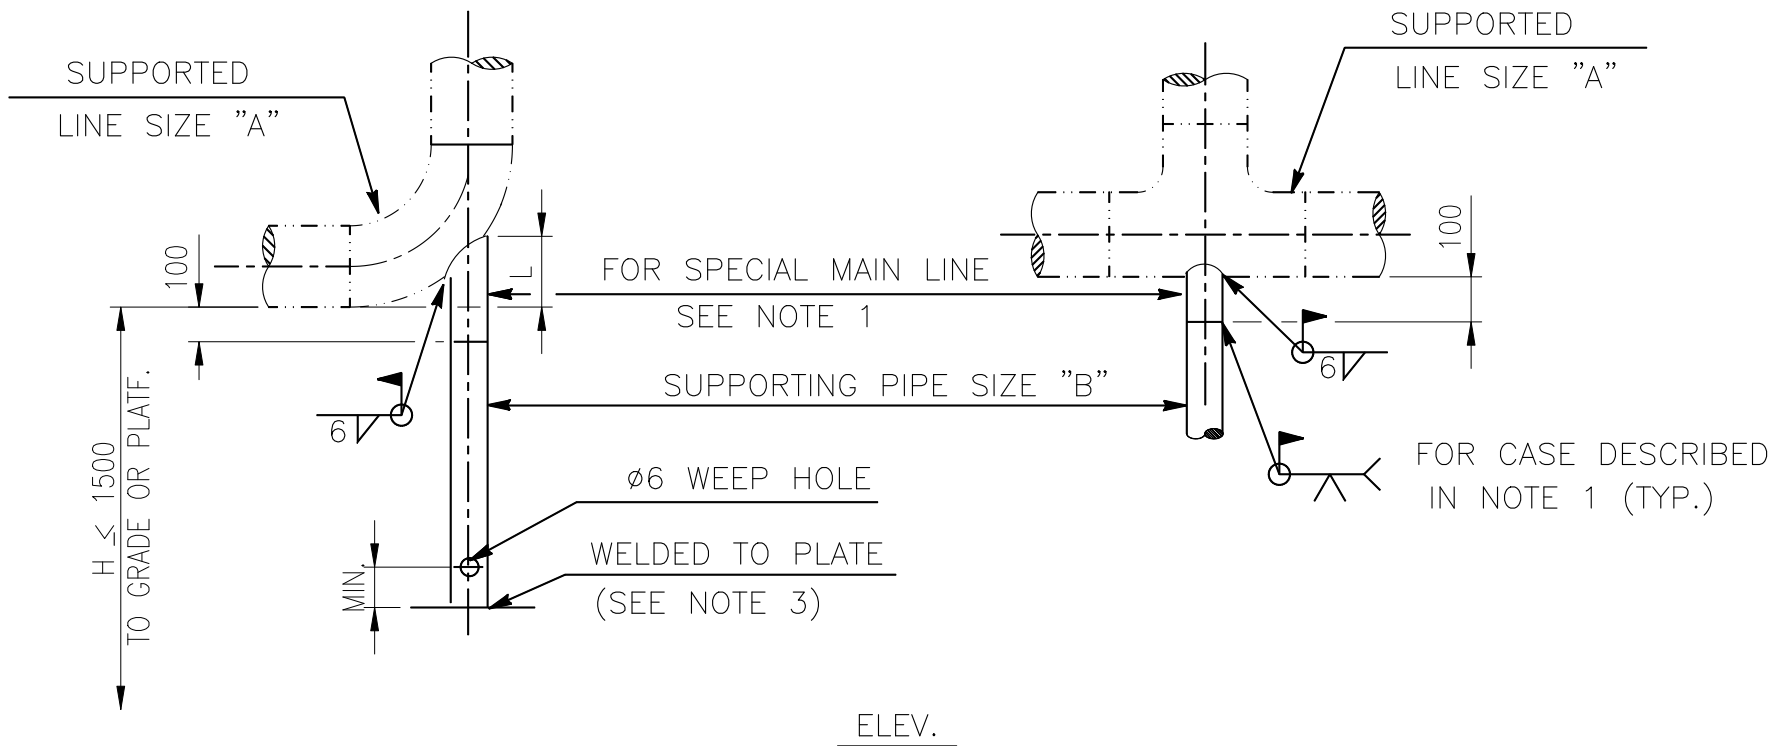

LINE SIZE "A"	PIPE SIZE "B"	L (NOTE 5)	LINE SIZE "A"	PIPE SIZE "B"	L (NOTE 5)
2"	1 1/2" SCH.80	71	30"	18"STD.WT	859
3"	2"SCH.40	93	32"	24"STD.WT	1060
4"	3"SCH.40	139	34"	24"STD.WT	1077
6"	4"SCH.40	186	36"	24"STD.WT	1099
8"	6"SCH.40	271	38"	24"STD.WT	1099
10"	8"SCH.40	353	40"	24"STD.WT	1147
12"	8"SCH.40	370	42"	24"STD.WT	1173
14"	10"SCH.40	473	44"	24"STD.WT	1200
16"	10"SCH.40	491	46"	28"STD.WT	1329
18"	12"STD.WT	572	48"	28"STD.WT	1355
20"	12"STD.WT	594	50"	28"STD.WT	1382
22"	14"STD.WT	652			
24"	14"STD.WT	677			
26"	16"STD.WT	756			
28"	16"STD.WT	782			

NOTES :

1. FOR ALLOY STEEL STAINLESS STEEL & STRESS RELIEF LINES, THE MATERIALS SHALL BE THE SAME AS MAIN LINES.

2. DIMENSION "H" SHALL BE CUT TO SUIT IN FIELD .

3. THIS TYPE SHALL BE USED WITH M-42 TO DETERMINE THE LOWER COMPONENT TYPE .

4. DESIGNATION NUMBER DENOTE AS FOLLOWS:

01-2B-05B

DENOTE THE LOWER COMPONENT TYPE SEE M-42

DENOTE DIMENSION "H" (IN 100mm) (SEE NOTE 6)

DENOTE SUPPORTED LINE SIZE "A"

DENOTE TYPE NO.

5. DIMENSION "L" IS BASED ON LONG RADIUS ELBOW TO WHICH DUMMY PIPE IS WELDED.

6. IF ONE OF THE LOWER COMPONENT TYPE-A,B,E,G IS USED, DIMENSION "H" SHALL BE COUNTED FROM THE ELEVATION OF THE LOWEST POINT OF PAVING.

中威工程顧問股份有限公司 CHUNG WEI ENGINEERING CONSULTING CO., LTD.						ENGINEERING STANDARD	
						HP6-DSD-A4-500-001	
BY	SHIH		CHK.	YANG		D-1	
DATE	7/15/'24		APPR.	CHEN			
DETAIL OF PIPE SUPPORT TYPE-01						REV. 1	

FILE: D-1M.DWG