


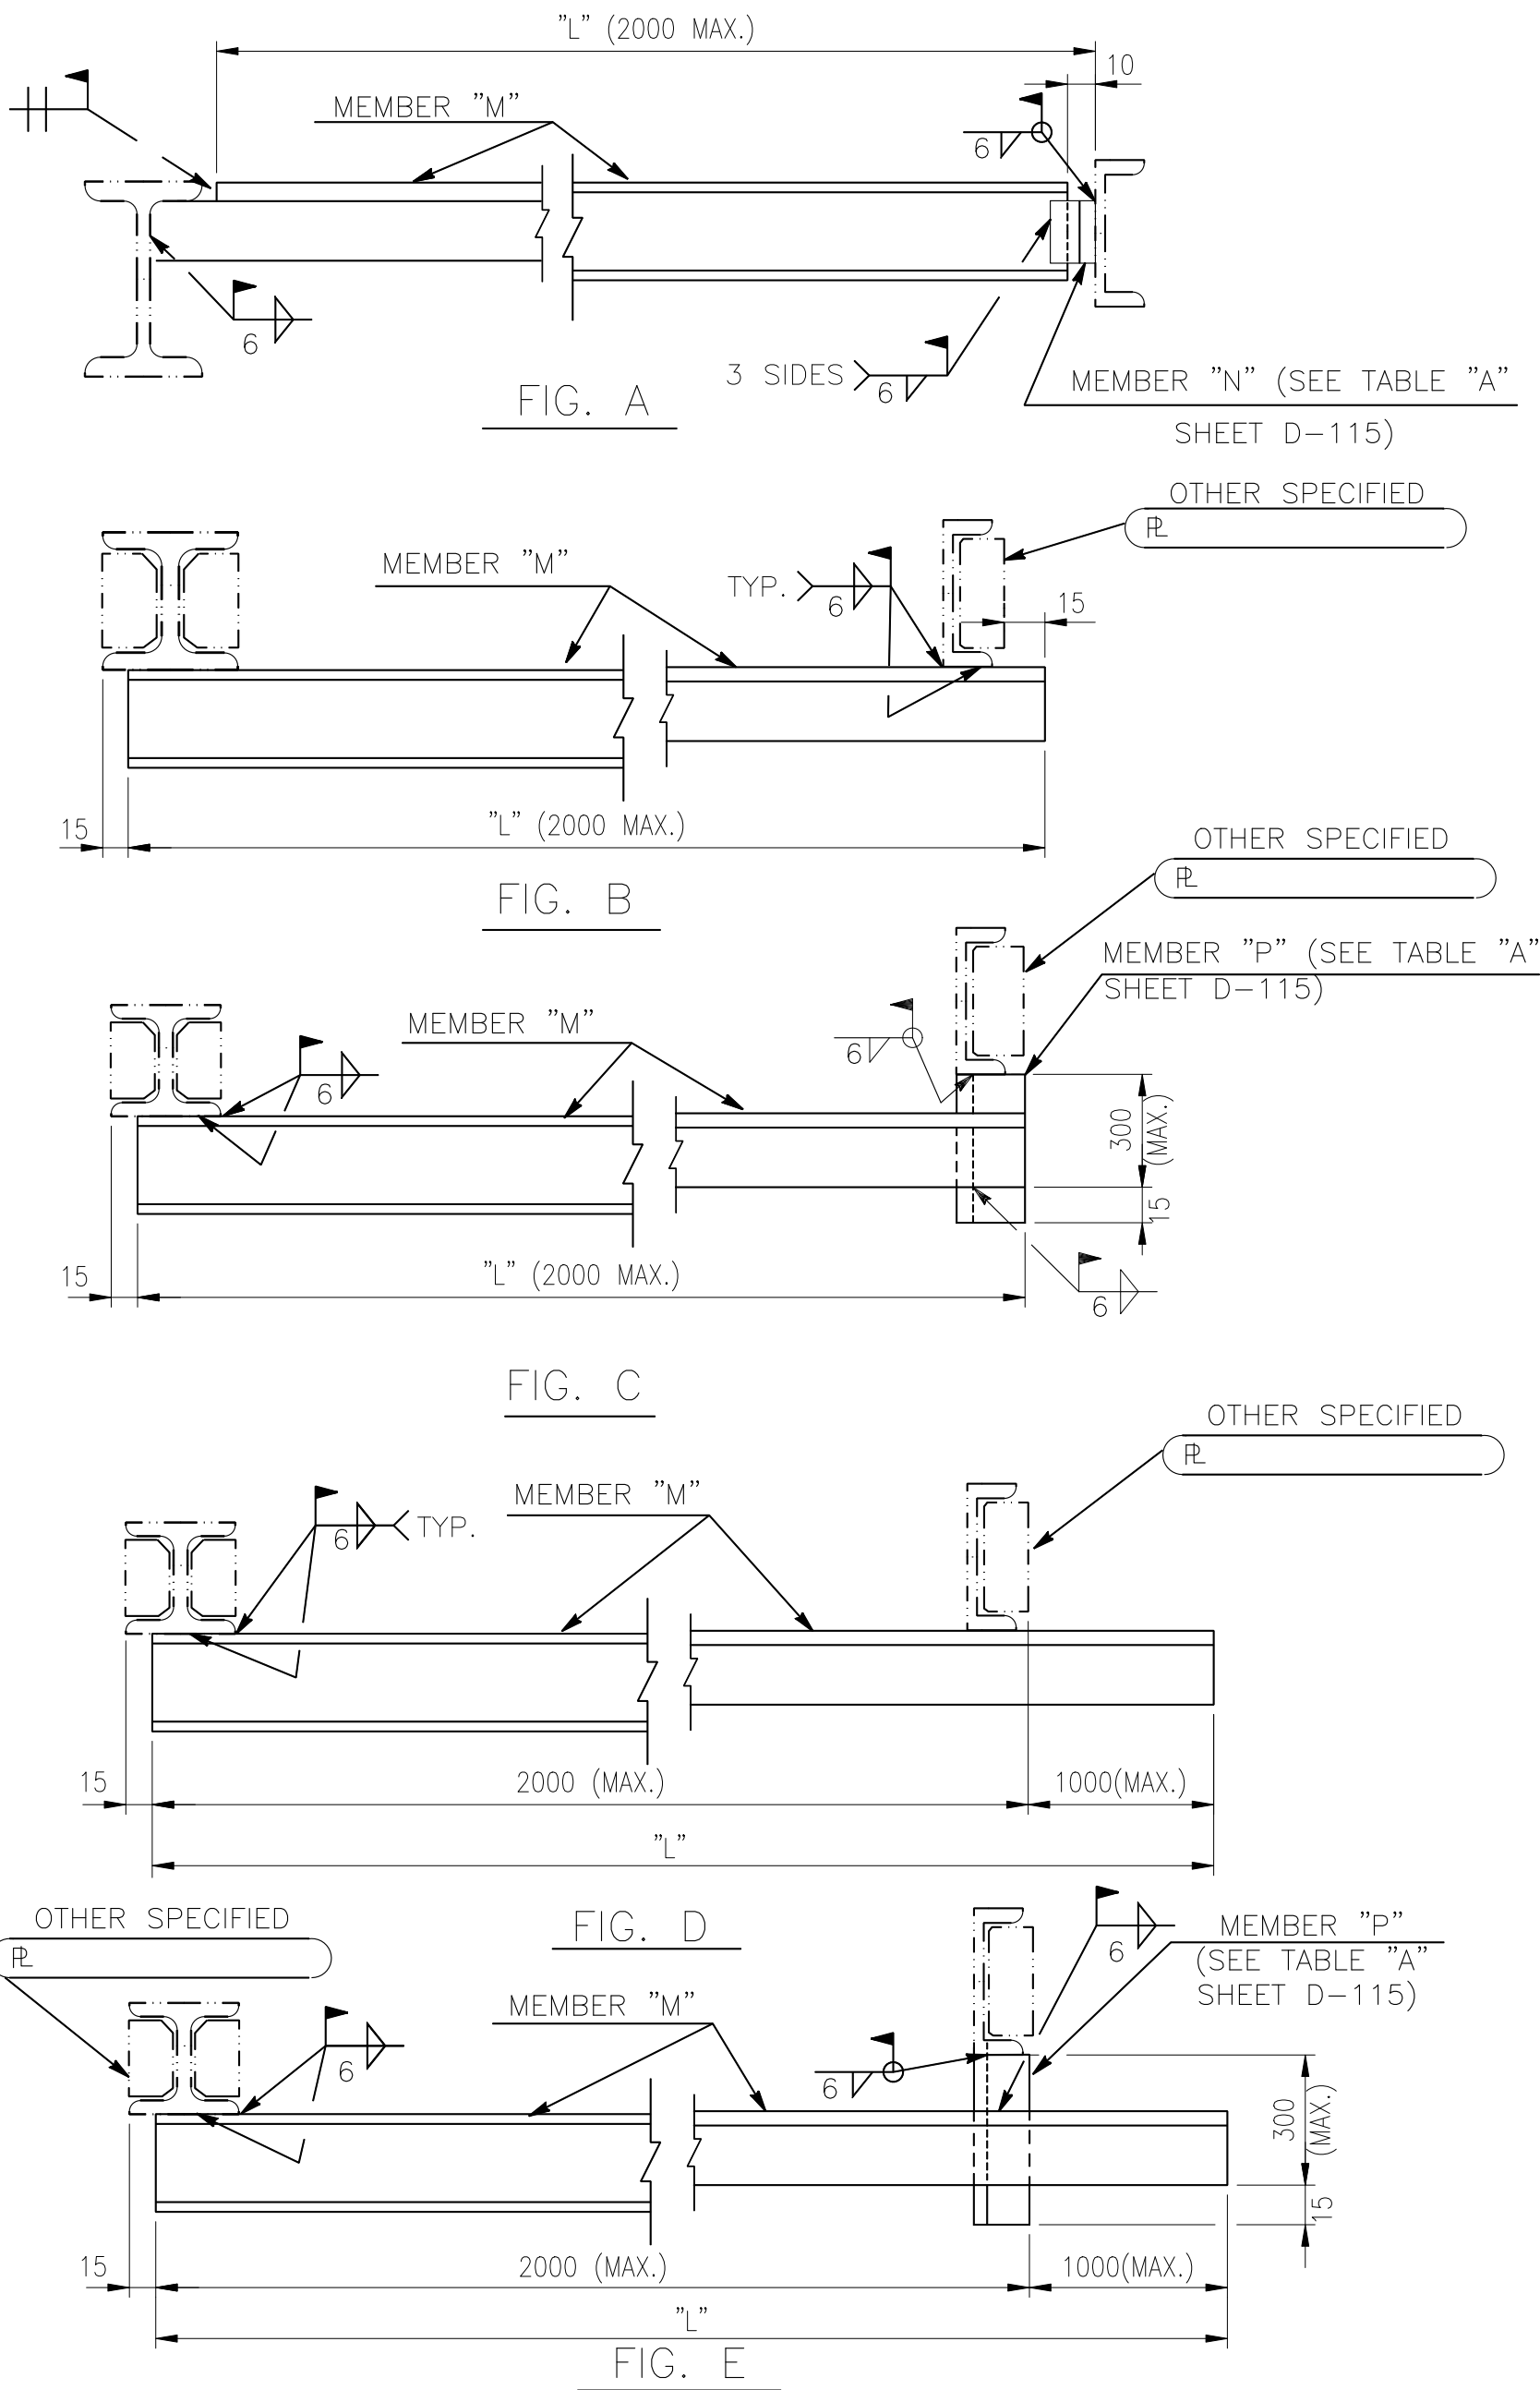

FILE: D-114M.DWG

中威工程顧問股份有限公司 CHUNG WEI ENGINEERING CONSULTING CO., LTD.						ENGINEERING STANDARD	
DETAIL OF PIPE SUPPORT TYPE-105 (1 OF 2)						HP6-DSD-A4-500-001	
						D-114	REV. 1
BY	SHIH		CHK.	YANG			
DATE	7/15/'24		APPR.	CHEN			