



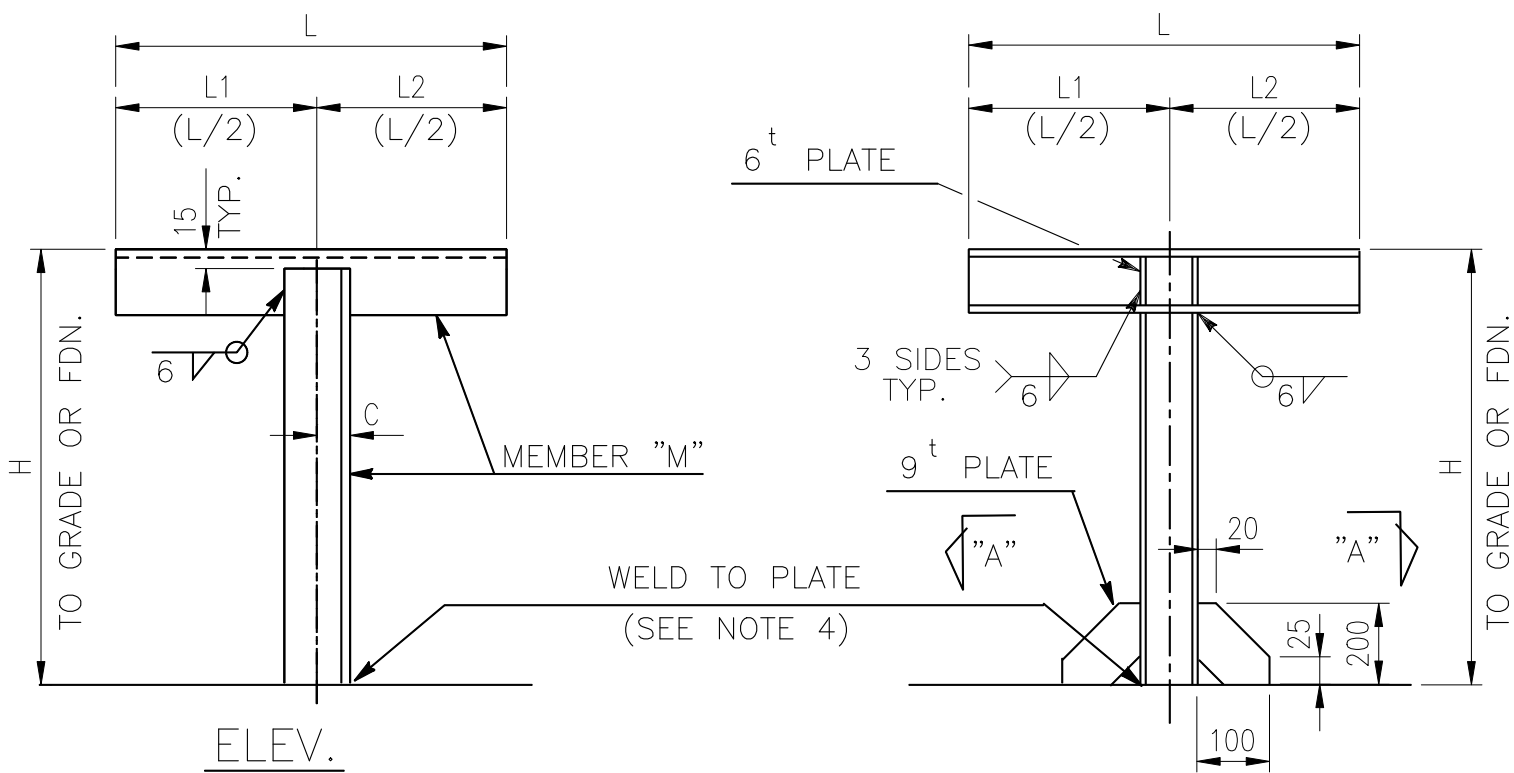

DIMENSION (mm)

MEMBER "M"	L (MAX.)	H (MAX.)	C
L50X50X6	300	500	30
L75X75X9	500	500	35
L100X100X10	700	1000	50
H150X150X10	600	2500	—

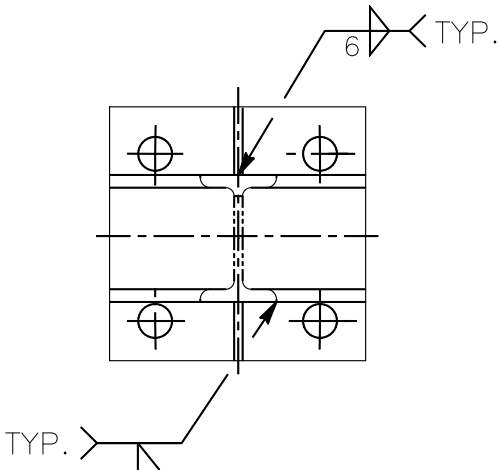


SECTION "A"~"A"

NOTES:

1. DESIGNATION DENOTE AS FOLLOWS:

27-L75-0505L-0401

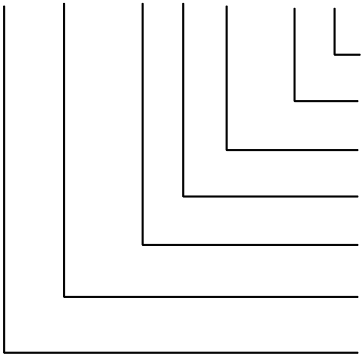

- MODIFY DIMENSION "L2" (IN 100mm) IF ANY
- MODIFY DIMENSION "L1" (IN 100mm) IF ANY
- DENOTE THE LOWER COMPONENT TYPE SEE M-42
- DENOTE DIM. "H" (IN 100 mm)
- DENOTE DIM. "L" (IN 100 mm)
- DENOTE MEMBER "M"
- DENOTE TYPE NO.

2. DIMENSION "H" & "L" SHALL BE CUT TO SUIT IN FIELD.

3. IF THE FOUNDATION IS NOT USED IN THIS DETAIL, DIMENSION "H" SHALL BE COUNTED FROM THE ELEVATION OF THE LOWEST POINT OF PAVING.

4. THIS TYPE SHALL BE USED WITH M-42 TO DETERMINE THE LOWER COMPONENT TYPE. IN THIS DETAIL, USE TYPE-L & P ONLY.

FILE: D-30M.DWG

中威工程顧問股份有限公司 CHUNG WEI ENGINEERING CONSULTING CO., LTD.						ENGINEERING STANDARD	
						HP6-DSD-A4-500-001	
BY	SHIH		CHK.	YANG		D-30	REV. 1
DATE	7/15/'24		APPR.	CHEN			

DETAIL OF PIPE SUPPORT
TYPE-27