


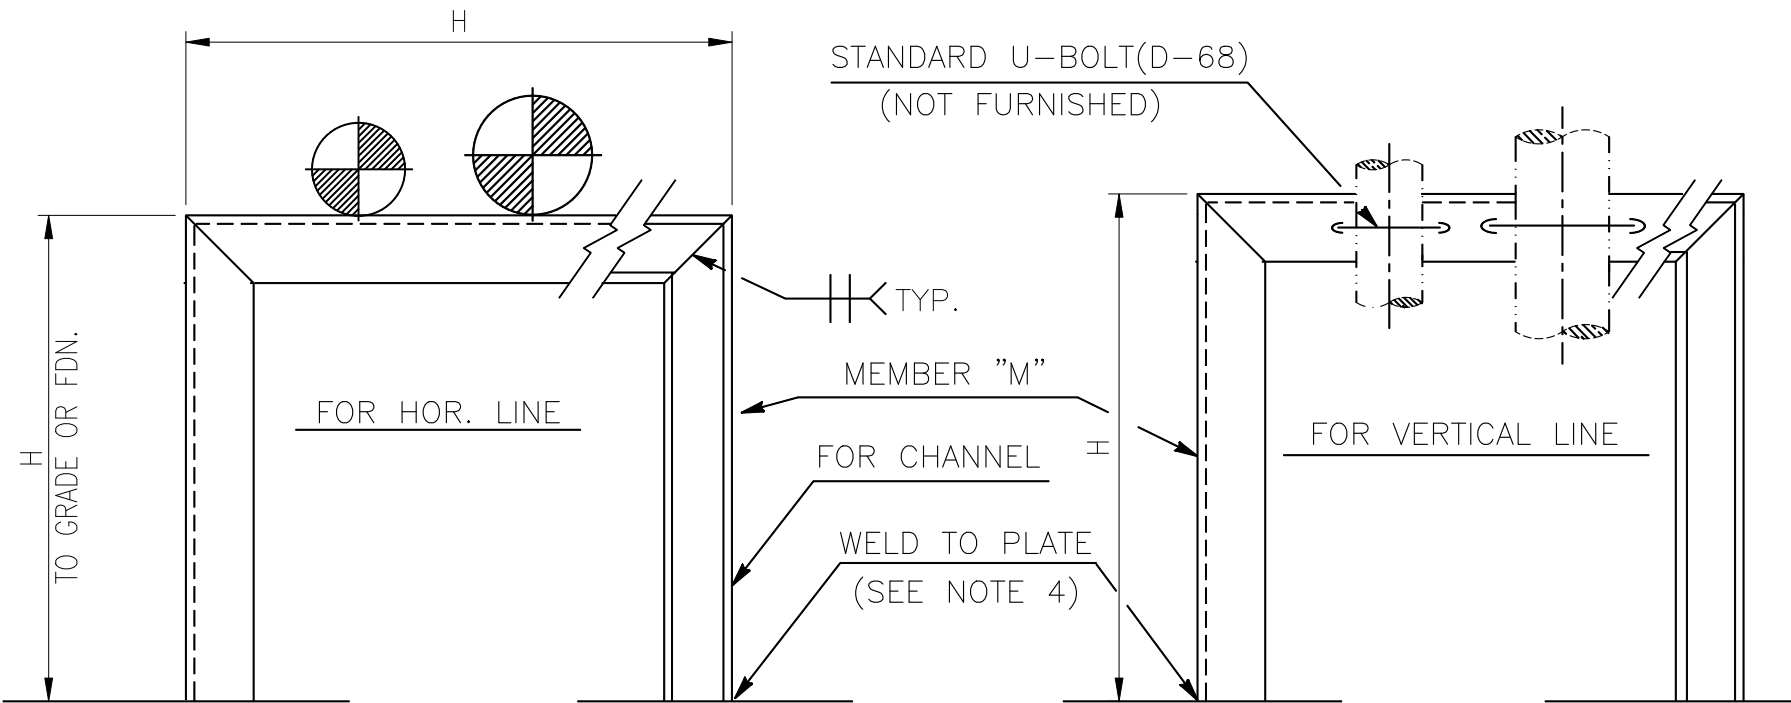


ELEV.

MEMBER "M"	L (MAX.)	H (MAX.)
L50X50X6	1000	500
L75X75X9	1000	1500
C125X65X6	1500	1500
C150X75X9	1500	1500
H250X125X6X9	1500	1500

NOTES:

1. DIMENSION "H" & "L" SHALL BE CUT TO SUIT IN FIELD .
2. DESIGNATION NUMBER DENOTES AS FOLLOWS:

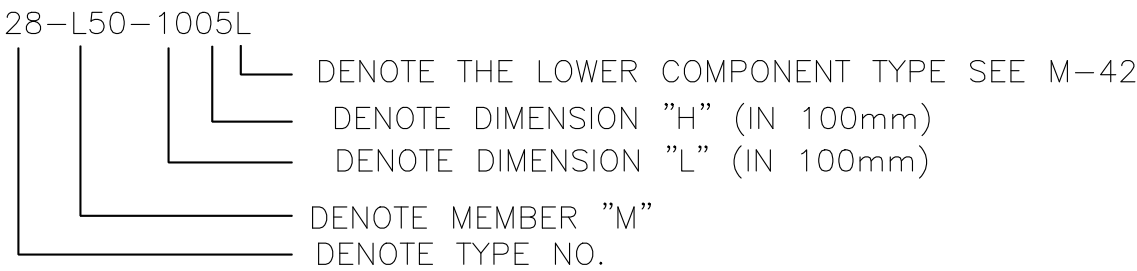

3. IF THE FOUNDATION IS NOT USED IN THIS DETAIL, DIMENSION "H" SHALL BE COUNTED FROM THE ELEVATION OF THE LOWEST POINT OF PAVING.
4. THIS TYPE SHALL BE USED WITH M-42 TO DETERMINE THE LOWER COMPONENT TYPE. IN THIS DETAIL, USE TYPE-L & P ONLY.

FILE: D-31M.DWG

中威工程顧問股份有限公司 CHUNG WEI ENGINEERING CONSULTING CO., LTD.						ENGINEERING STANDARD	
						HP6-DSD-A4-500-001	
BY	SHIH		CHK.	YANG		D-31	REV. 1
DATE	7/15/'24		APPR.	CHEN			

DETAIL OF PIPE SUPPORT
TYPE-28