

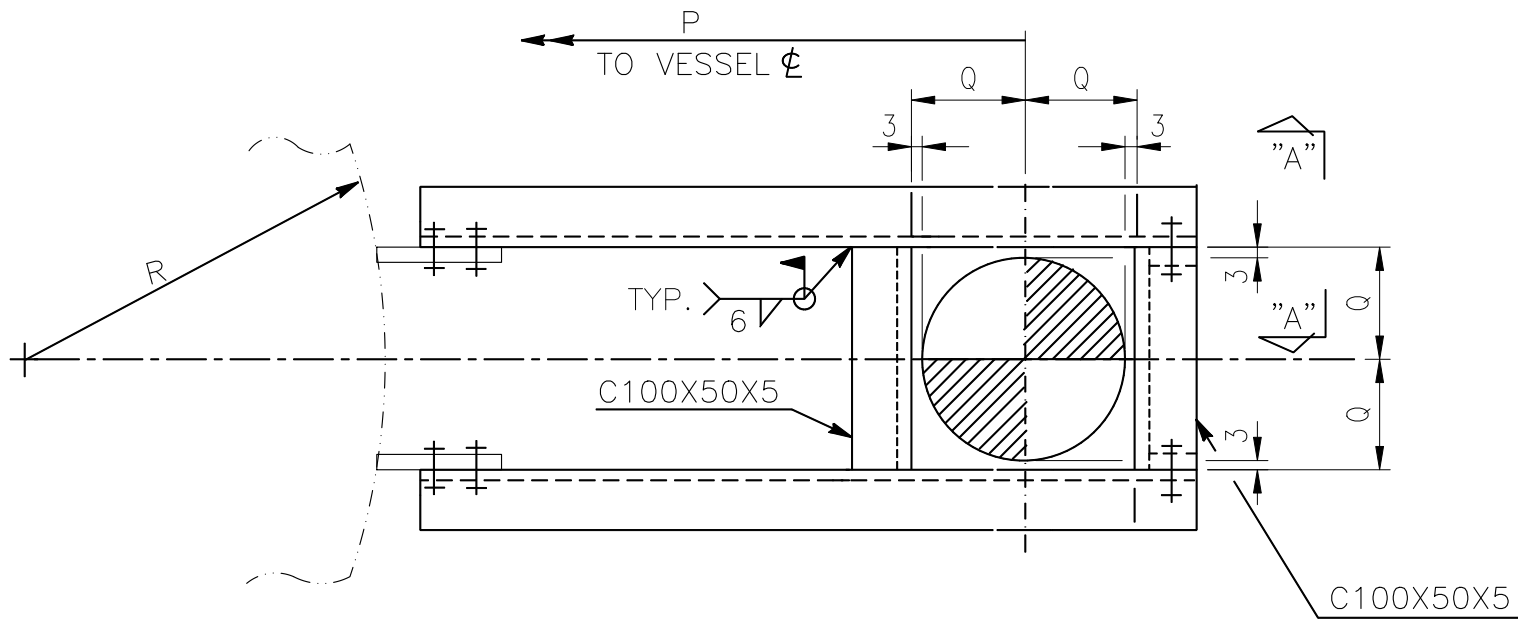


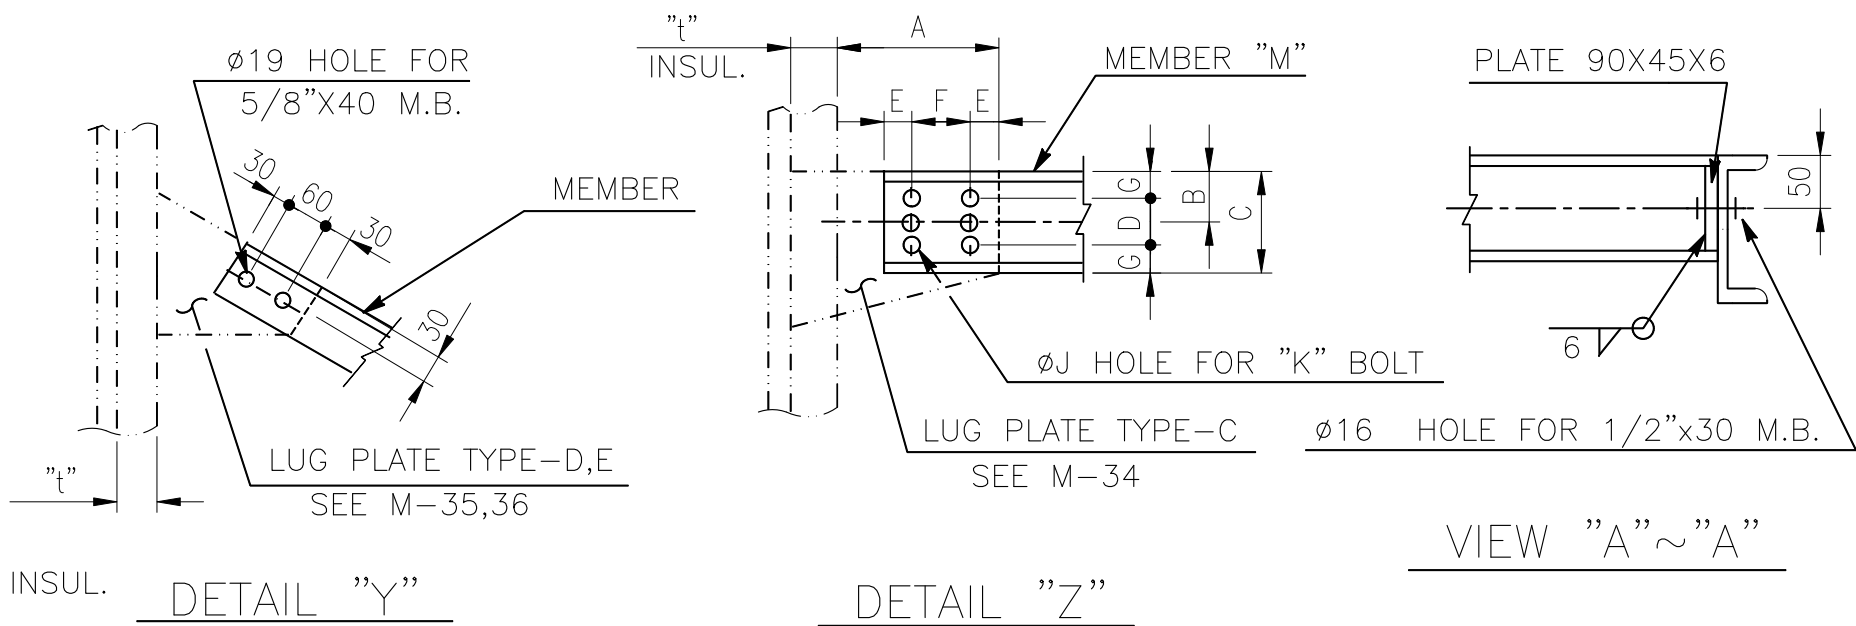

PLAN

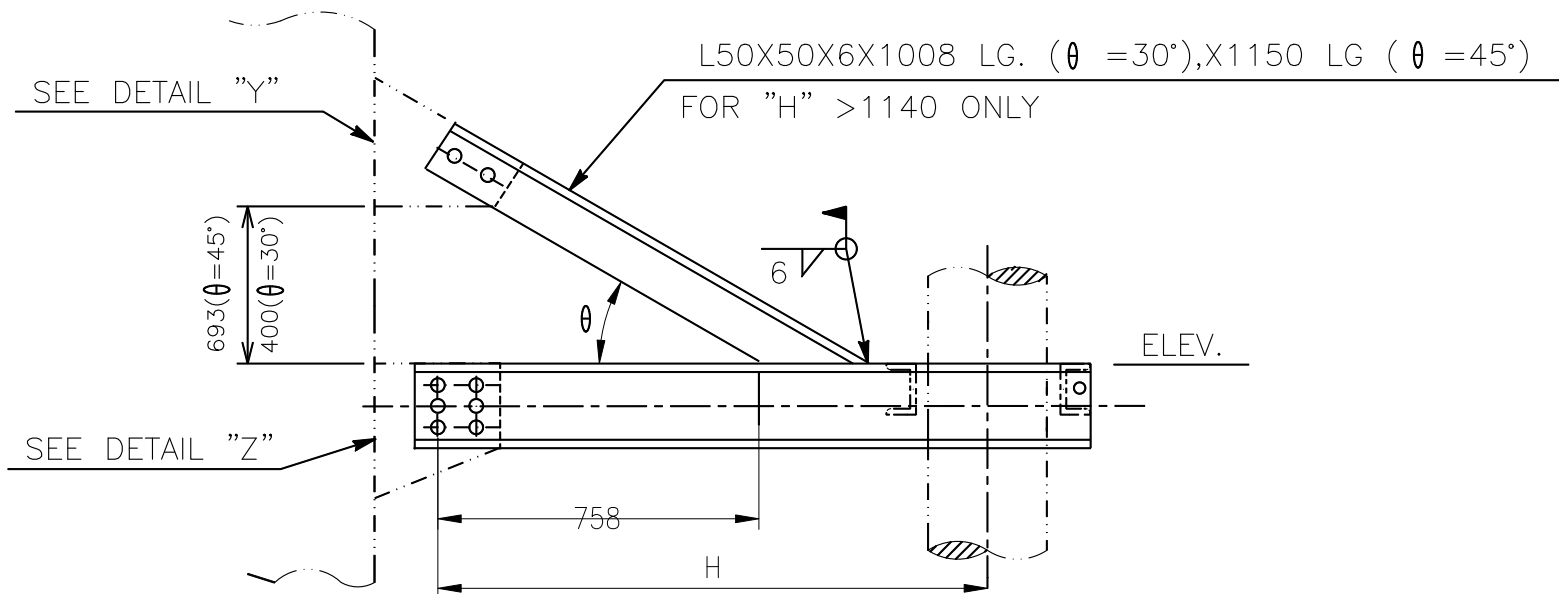

LINE SIZE	8"	10"	12"	14"
Q (mm)	113	140	165	181

FILE: D-54M.DWG

中威工程顧問股份有限公司 CHUNG WEI ENGINEERING CONSULTING CO., LTD.						ENGINEERING STANDARD	
DETAIL OF PIPE SUPPORT TYPE-45 (1 OF 2)						REV. 1	
						D-54	