


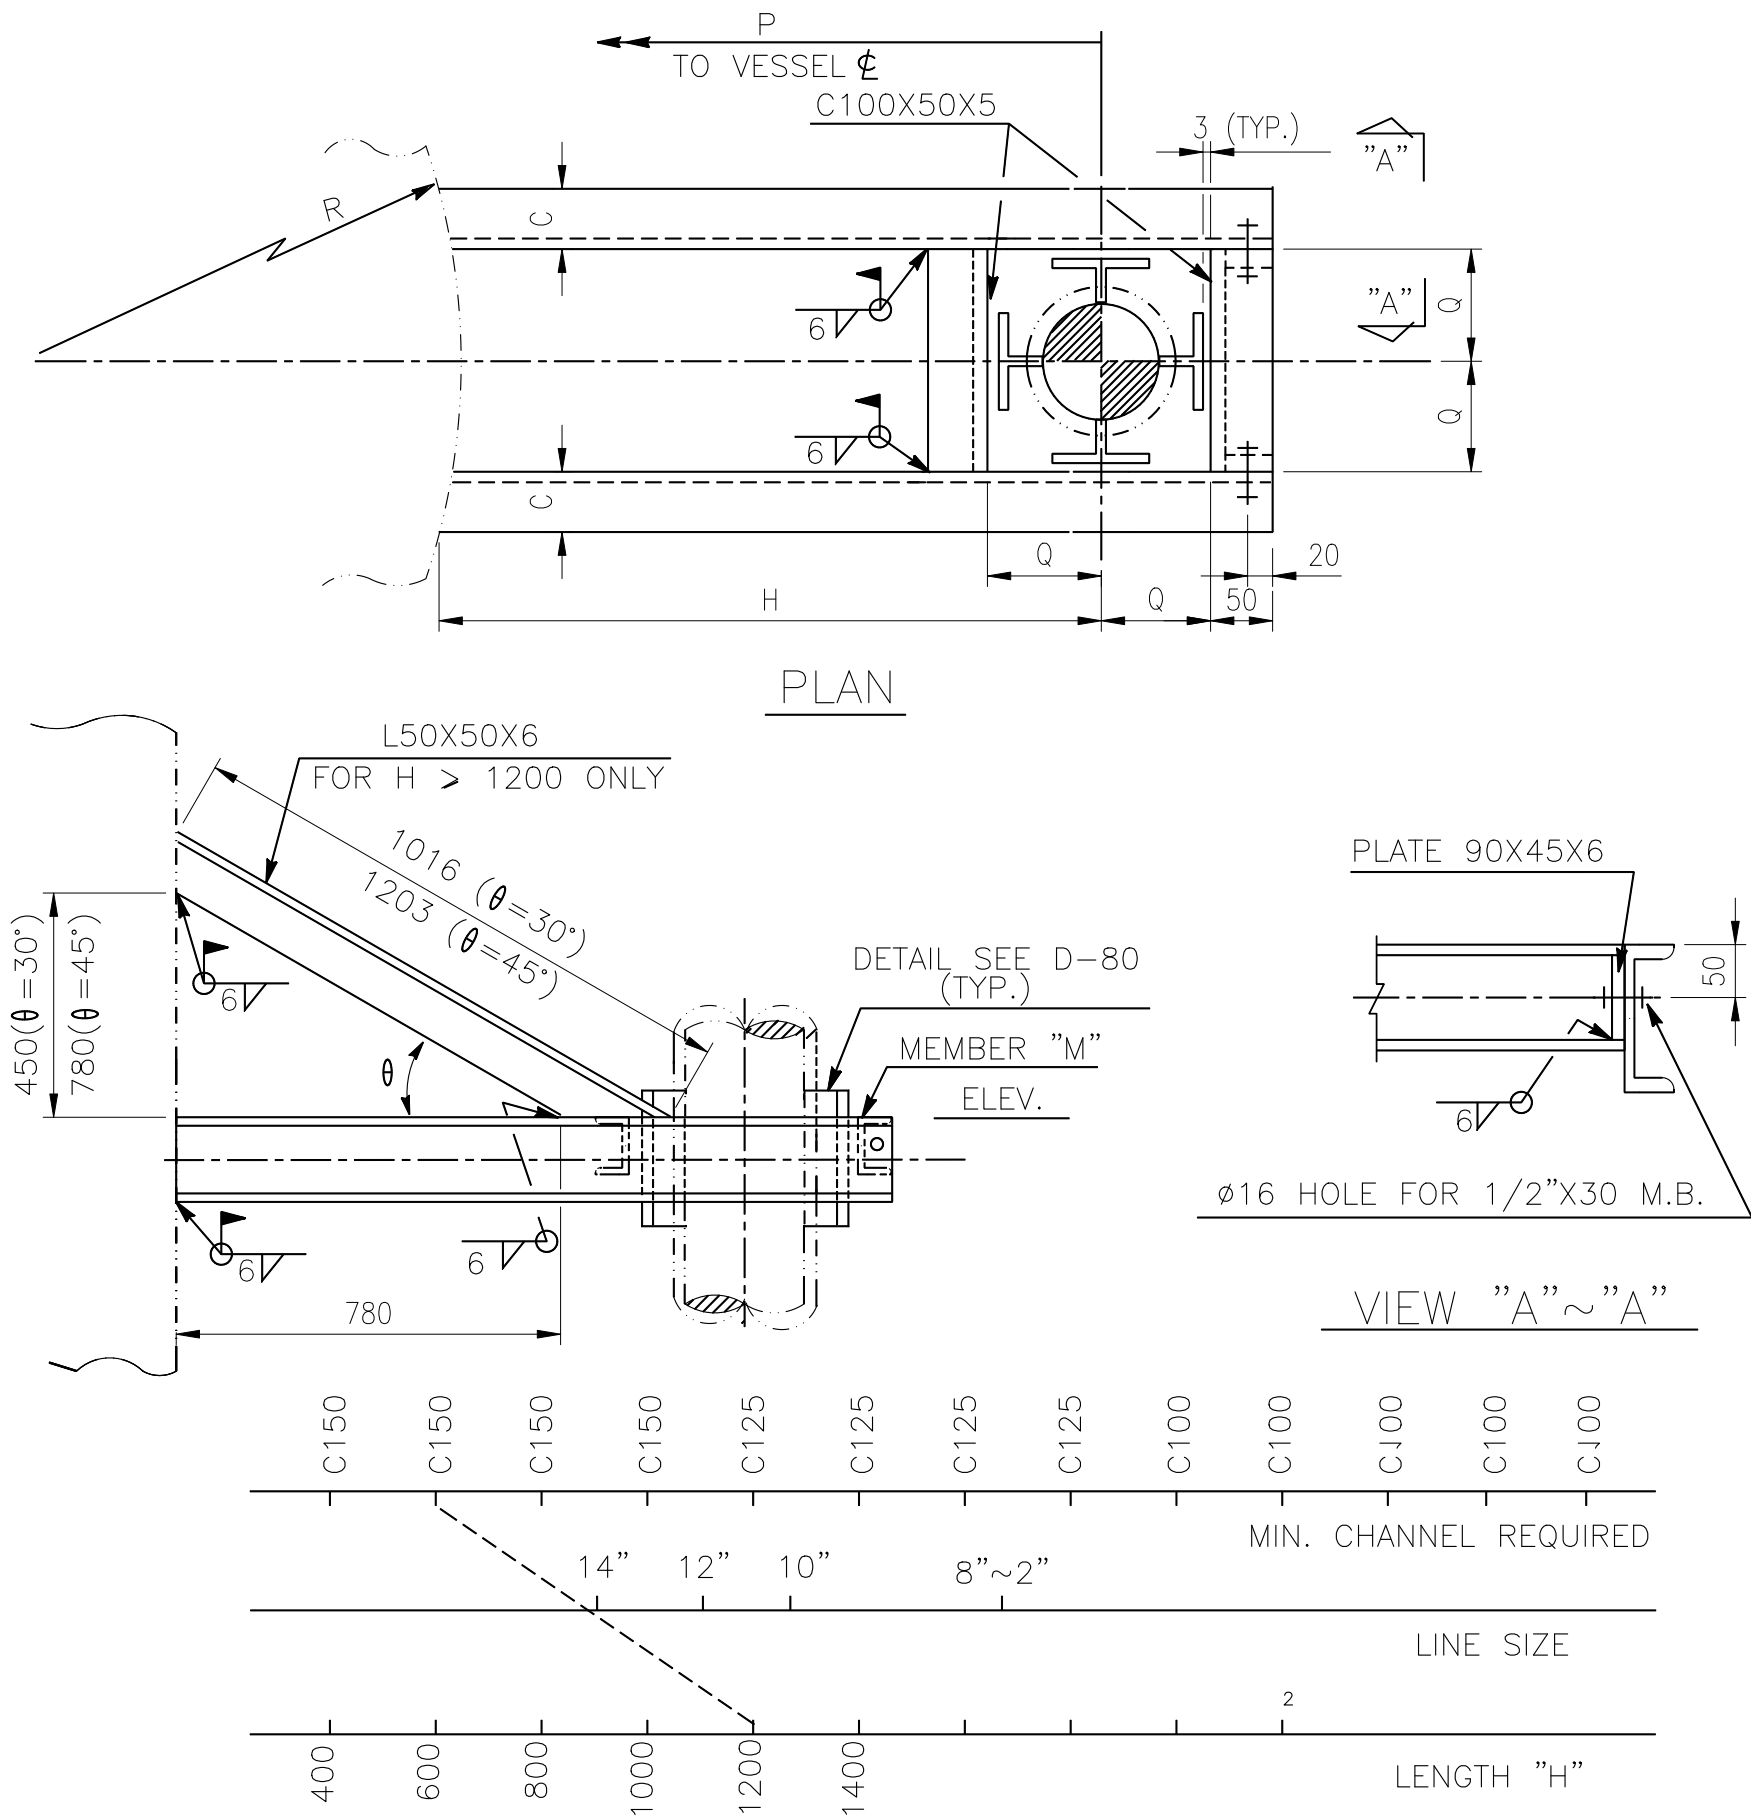

NOTES : 1. DESIGNATION NUMBER DENOTE AS FOLLOWS :

46-8B-C100-840 A OR B-175
DENOTE TYPE NO. | DENOTE SUPPORTED LINE SIZE | DENOTE LENGTH "H" (IN mm) | DENOTE MEMBER "M"
MODIFY DIMENSION "Q" (IN mm) IF ANY
SEE NOTE 2

2. A: FOR $\theta = 30^\circ$, B: FOR $\theta = 45^\circ$

中威工程顧問股份有限公司
CHUNG WEI ENGINEERING CONSULTING CO., LTD.

DETAIL OF PIPE SUPPORT
TYPE-46

ENGINEERING STANDARD

HP6-DSD-A4-500-001

BY	SHIH		CHK.	YANG	
DATE	7/15/'24		APPR.	CHEN	

D-56	REV. 1
------	-----------