


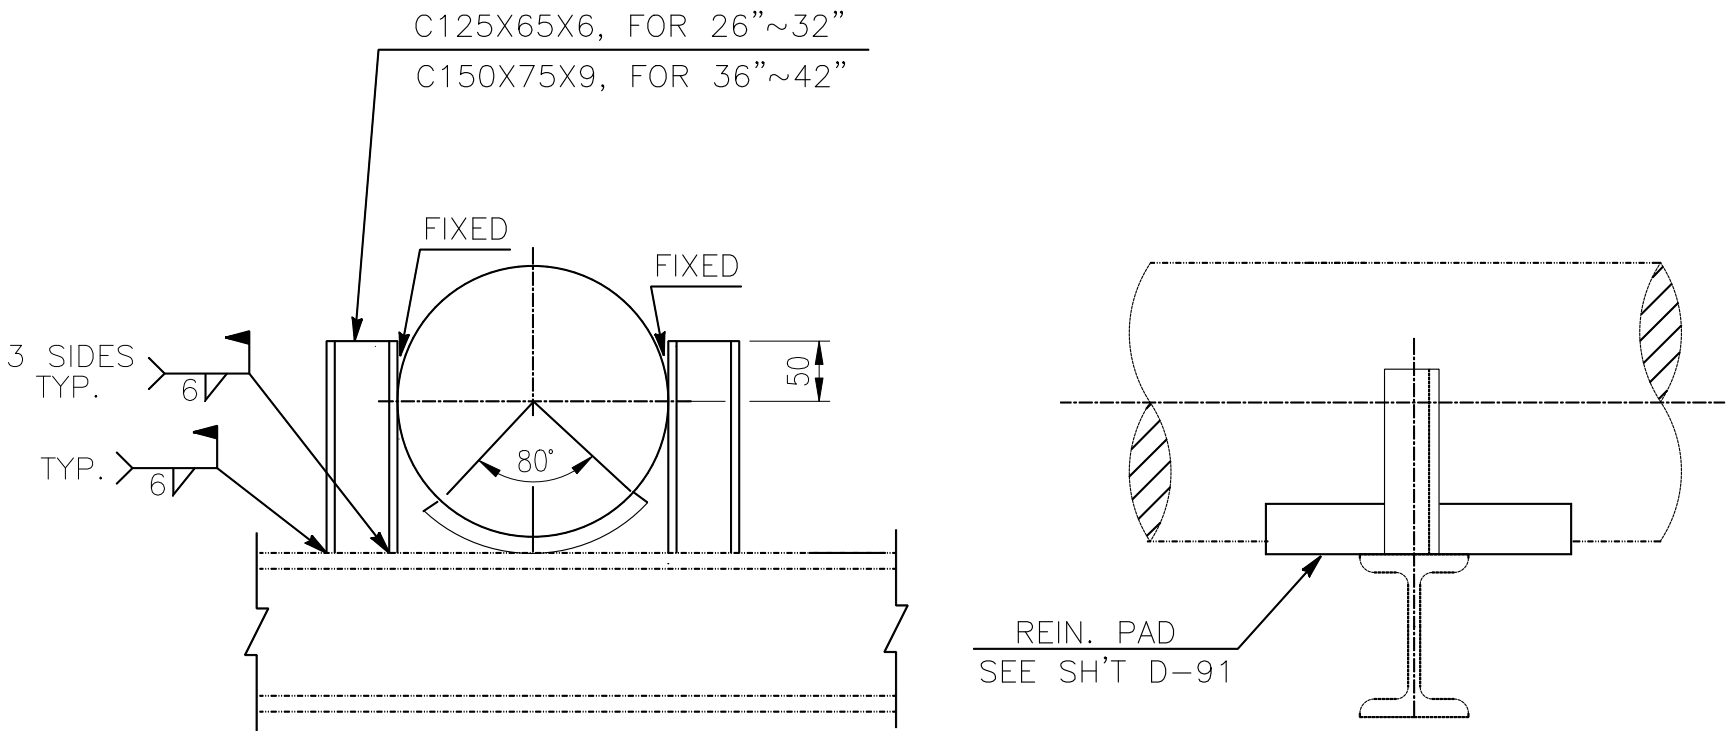

ELEV.

NOTES:

1. FOR DESIGNATION NUMBER OF SUPPORT SEE SH'T D-62.

FILE: D-62MA1.DWG

中威工程顧問股份有限公司 CHUNG WEI ENGINEERING CONSULTING CO., LTD.						ENGINEERING STANDARD	
						HP6-DSD-A4-500-001	
BY	SHIH		CHK.	YANG		DETAIL OF PIPE SUPPORT TYPE-51A (2 OF 2)	REV.
DATE	7/15/'24		APPR.	CHEN			1