


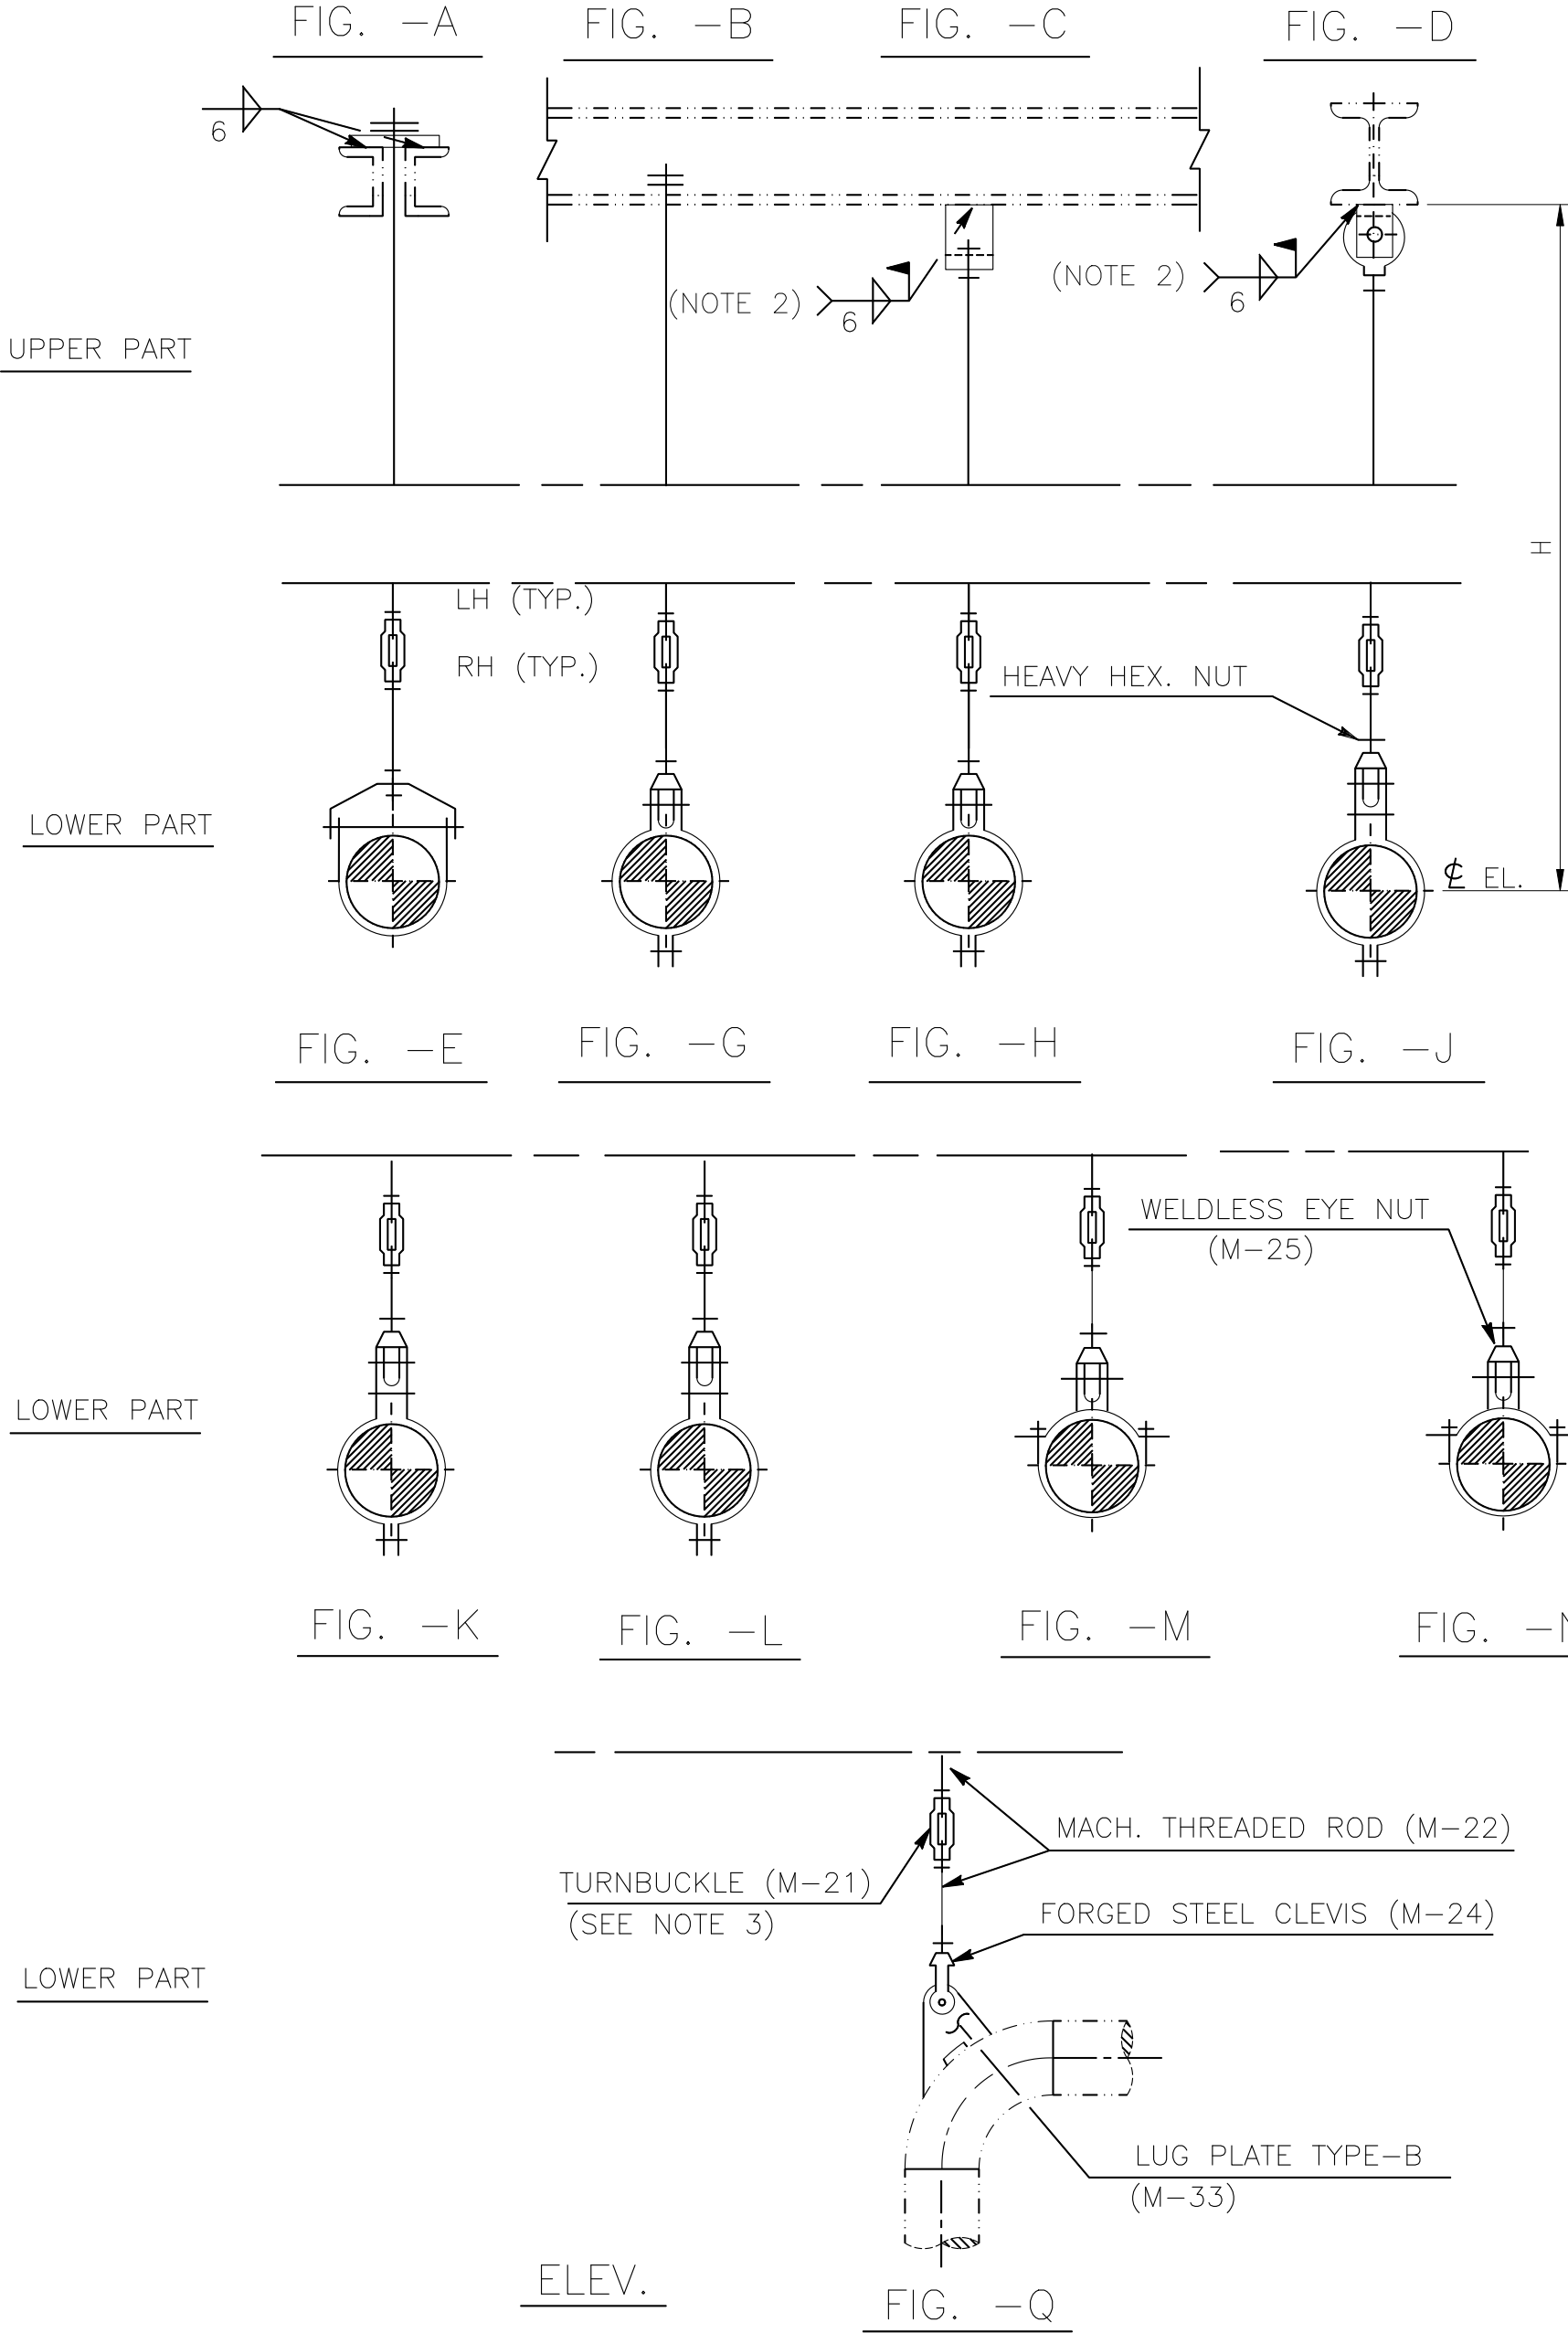

FILE: D-75M.DWG	中威工程顧問股份有限公司 CHUNG WEI ENGINEERING CONSULTING CO., LTD.					DETAIL OF PIPE SUPPORT TYPE-62 (1 OF 2)		ENGINEERING STANDARD		
								HP6-DSD-A4-500-001		
	BY	SHIH		CHK.	YANG				D-75	REV. 1
	DATE	7/15/'24		APPR.	CHEN					

FILE: D-75M.DWG