


FOR PIPE SIZE 26" ~ 42"

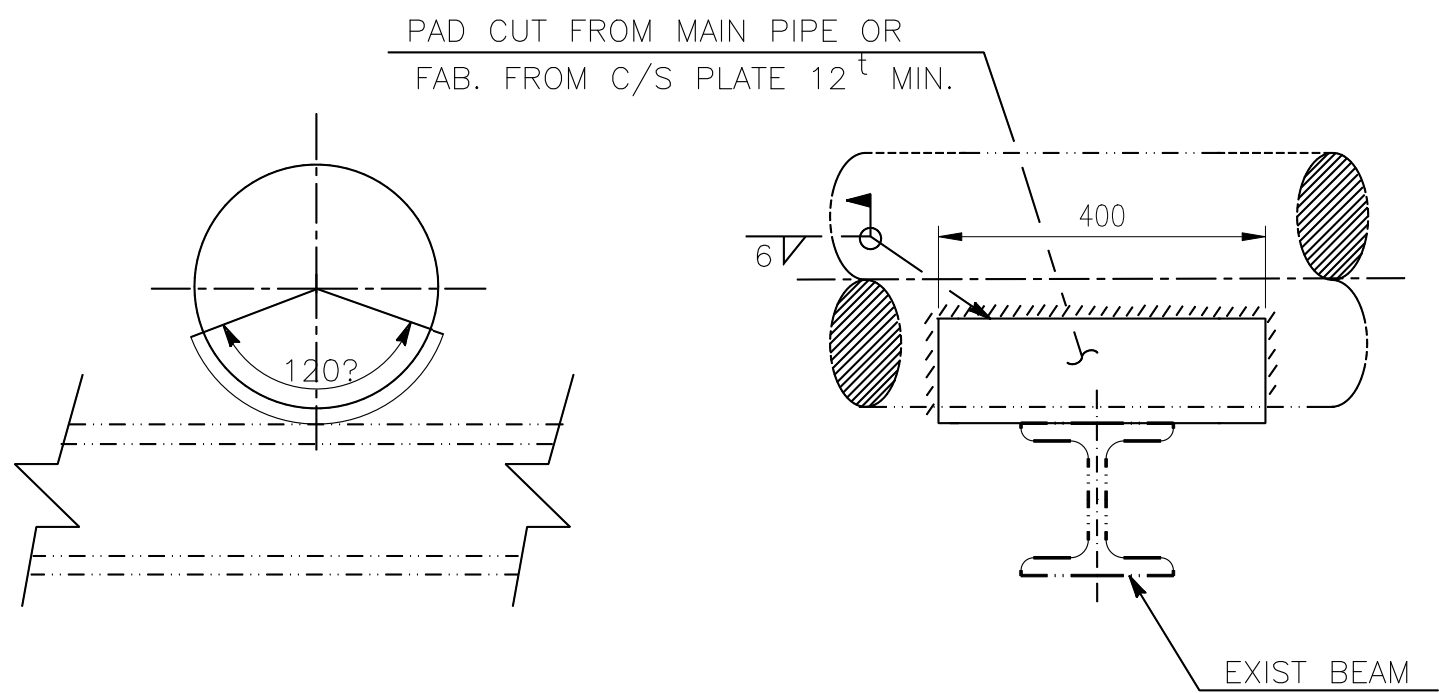

NOTE: DESIGNATION NUMBER DENOTE AS FOLLOWS:

76 - 30B

└─┬─┘ DENOTE LINE SIZE

└─┬─┘ DENOTE TYPE NO.

FILE: D-91M.DWG

中威工程顧問股份有限公司 CHUNG WEI ENGINEERING CONSULTING CO., LTD.						ENGINEERING STANDARD	
						HP6-DSD-A4-500-001	
BY	SHIH		CHK.	YANG		D-91	REV.
DATE	7/15/'24		APPR.	CHEN			1

DETAIL OF PIPE SUPPORT
TYPE-76