


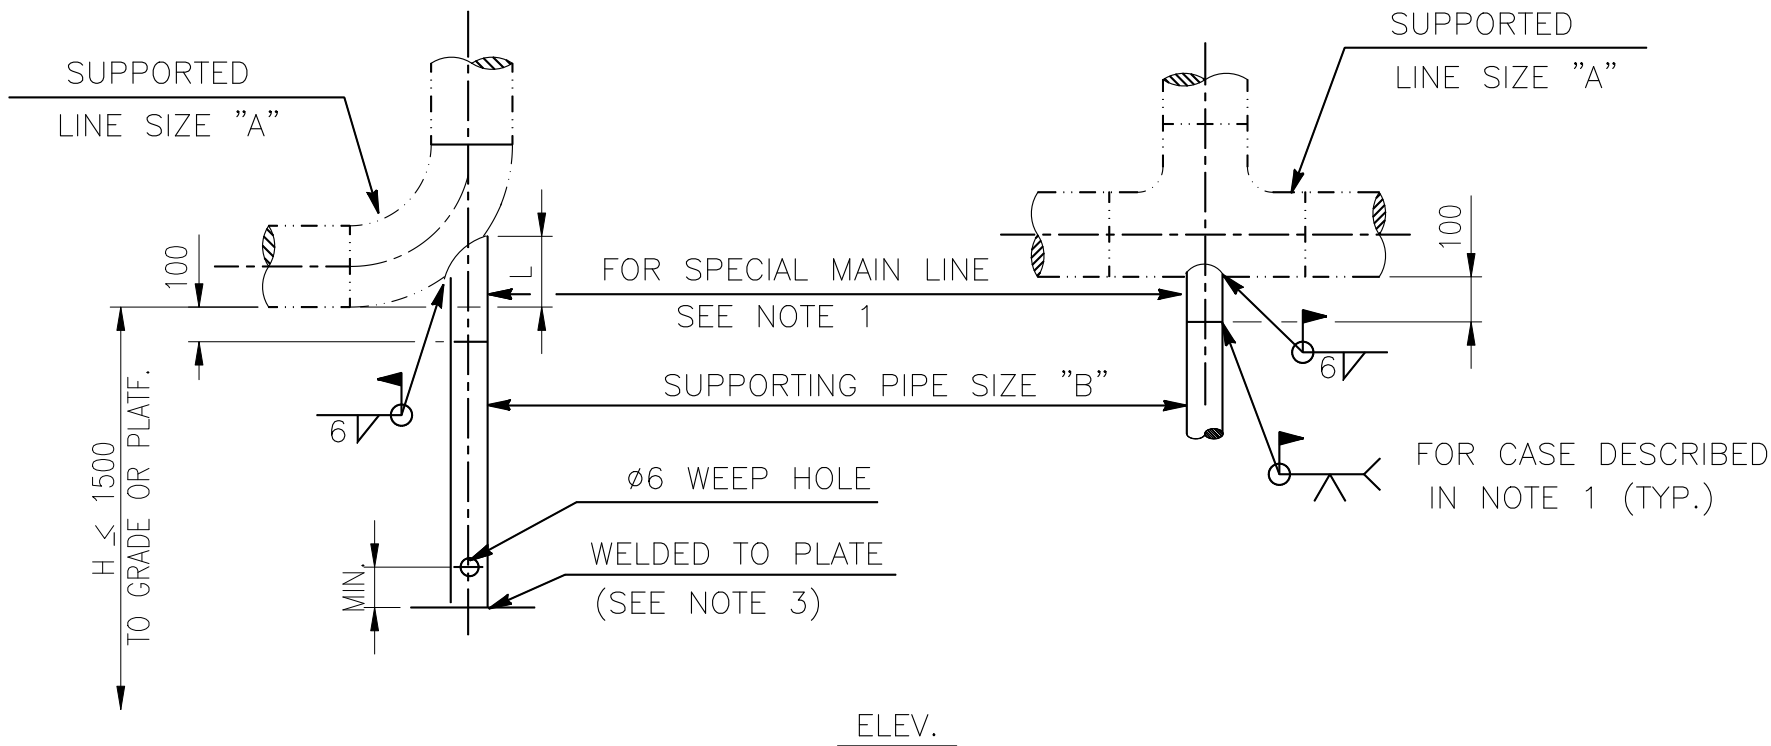

| LINE SIZE<br>"A" | PIPE SIZE<br>"B" | L<br>(NOTE 5) | LINE SIZE<br>"A" | PIPE SIZE<br>"B" | L<br>(NOTE 5) |
|------------------|------------------|---------------|------------------|------------------|---------------|
| 2"               | 1 1/2" SCH.80    | 71            | 30"              | 18"STD.WT        | 859           |
| 3"               | 2"SCH.40         | 93            | 32"              | 24"STD.WT        | 1060          |
| 4"               | 3"SCH.40         | 139           | 34"              | 24"STD.WT        | 1077          |
| 6"               | 4"SCH.40         | 186           | 36"              | 24"STD.WT        | 1099          |
| 8"               | 6"SCH.40         | 271           | 38"              | 24"STD.WT        | 1099          |
| 10"              | 8"SCH.40         | 353           | 40"              | 24"STD.WT        | 1147          |
| 12"              | 8"SCH.40         | 370           | 42"              | 24"STD.WT        | 1173          |
| 14"              | 10"SCH.40        | 473           | 44"              | 24"STD.WT        | 1200          |
| 16"              | 10"SCH.40        | 491           | 46"              | 28"STD.WT        | 1329          |
| 18"              | 12"STD.WT        | 572           | 48"              | 28"STD.WT        | 1355          |
| 20"              | 12"STD.WT        | 594           | 50"              | 28"STD.WT        | 1382          |
| 22"              | 14"STD.WT        | 652           |                  |                  |               |
| 24"              | 14"STD.WT        | 677           |                  |                  |               |
| 26"              | 16"STD.WT        | 756           |                  |                  |               |
| 28"              | 16"STD.WT        | 782           |                  |                  |               |

NOTES :

1. FOR ALLOY STEEL STAINLESS STEEL & STRESS RELIEF LINES, THE MATERIALS SHALL BE THE SAME AS MAIN LINES.

2. DIMENSION "H" SHALL BE CUT TO SUIT IN FIELD .

3. THIS TYPE SHALL BE USED WITH M-42 TO DETERMINE THE LOWER COMPONENT TYPE .

4. DESIGNATION NUMBER DENOTE AS FOLLOWS:

01-2B-05B

DENOTE THE LOWER COMPONENT TYPE SEE M-42

DENOTE DIMENSION "H" (IN 100mm) (SEE NOTE 6)

DENOTE SUPPORTED LINE SIZE "A"

DENOTE TYPE NO.

5. DIMENSION "L" IS BASED ON LONG RADIUS ELBOW TO WHICH DUMMY PIPE IS WELDED.

6. IF ONE OF THE LOWER COMPONENT TYPE-A,B,E,G IS USED, DIMENSION "H" SHALL BE COUNTED FROM THE ELEVATION OF THE LOWEST POINT OF PAVING.

|                                                            |          |  |       |      |  |                      |           |
|------------------------------------------------------------|----------|--|-------|------|--|----------------------|-----------|
| 中威工程顧問股份有限公司<br>CHUNG WEI ENGINEERING CONSULTING CO., LTD. |          |  |       |      |  | ENGINEERING STANDARD |           |
|                                                            |          |  |       |      |  | HP6-DSD-A4-500-001   |           |
| BY                                                         | SHIH     |  | CHK.  | YANG |  | D-1                  | REV.<br>1 |
| DATE                                                       | 7/15/'24 |  | APPR. | CHEN |  |                      |           |

FILE: D-1M.DWG

DETAIL OF PIPE SUPPORT  
TYPE-01