


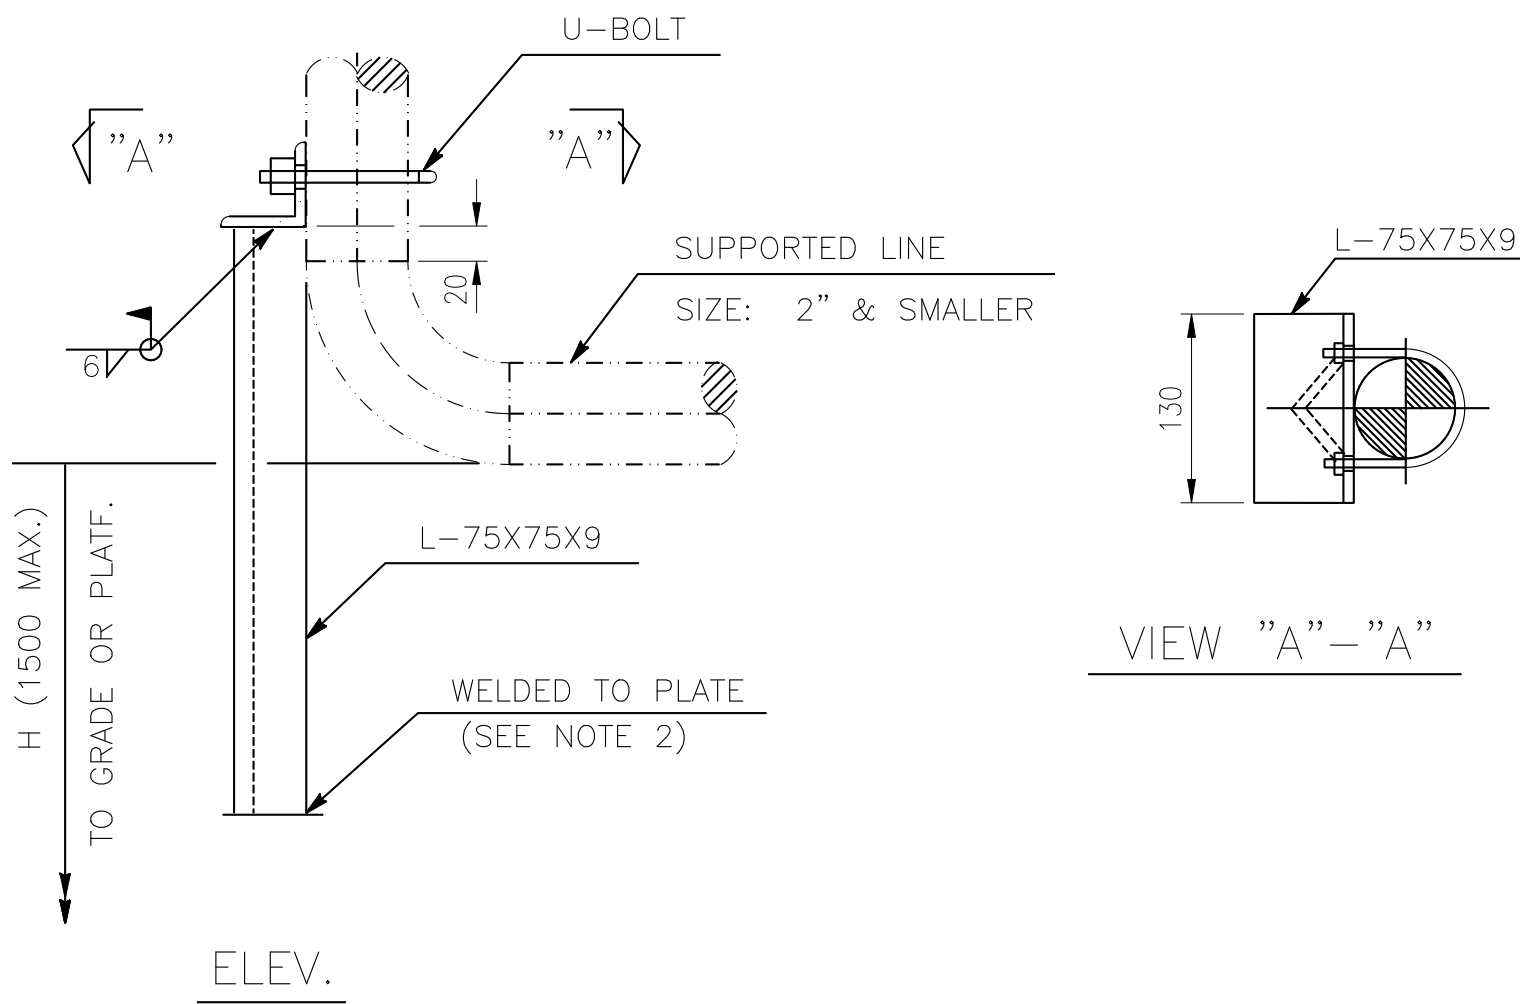

NOTES :

- DIMENSION "H" SHALL BE SUITED IN FIELD.
- THIS TYPE SHALL BE USED WITH M-42 TO DETERMINE THE LOWER COMPONENT TYPE. IN THIS DETAIL, USE TYPE- D,L,M,N,P & R ONLY.
- DESIGNATION NUMBER, DENOTE AS FOLLOWS :
03-1B-05N
DENOTE THE LOWER COMPONENT TYPE SEE M-42
DENOTE DIMENSION "H" (IN 100 mm) (SEE NOTE 4)
DENOTE SUPPORTED LINE SIZE
DENOTE TYPE NO.
- IF ONE OF THE LOWER COMPONENT TYPE-L, M IS USED, DIMENSION "H" SHALL BE COUNTED FROM THE ELEVATION OF THE LOWEST POINT OF PAVING.

FILE: D-3M.DWG

中威工程顧問股份有限公司 CHUNG WEI ENGINEERING CONSULTING CO., LTD.						ENGINEERING STANDARD	
DETAIL OF PIPE SUPPORT TYPE-03						HP6-DSD-A4-500-001	
						D-3	REV. 1
BY	SHIH		CHK.	YANG			
DATE	7/15/'24		APPR.	CHEN			