


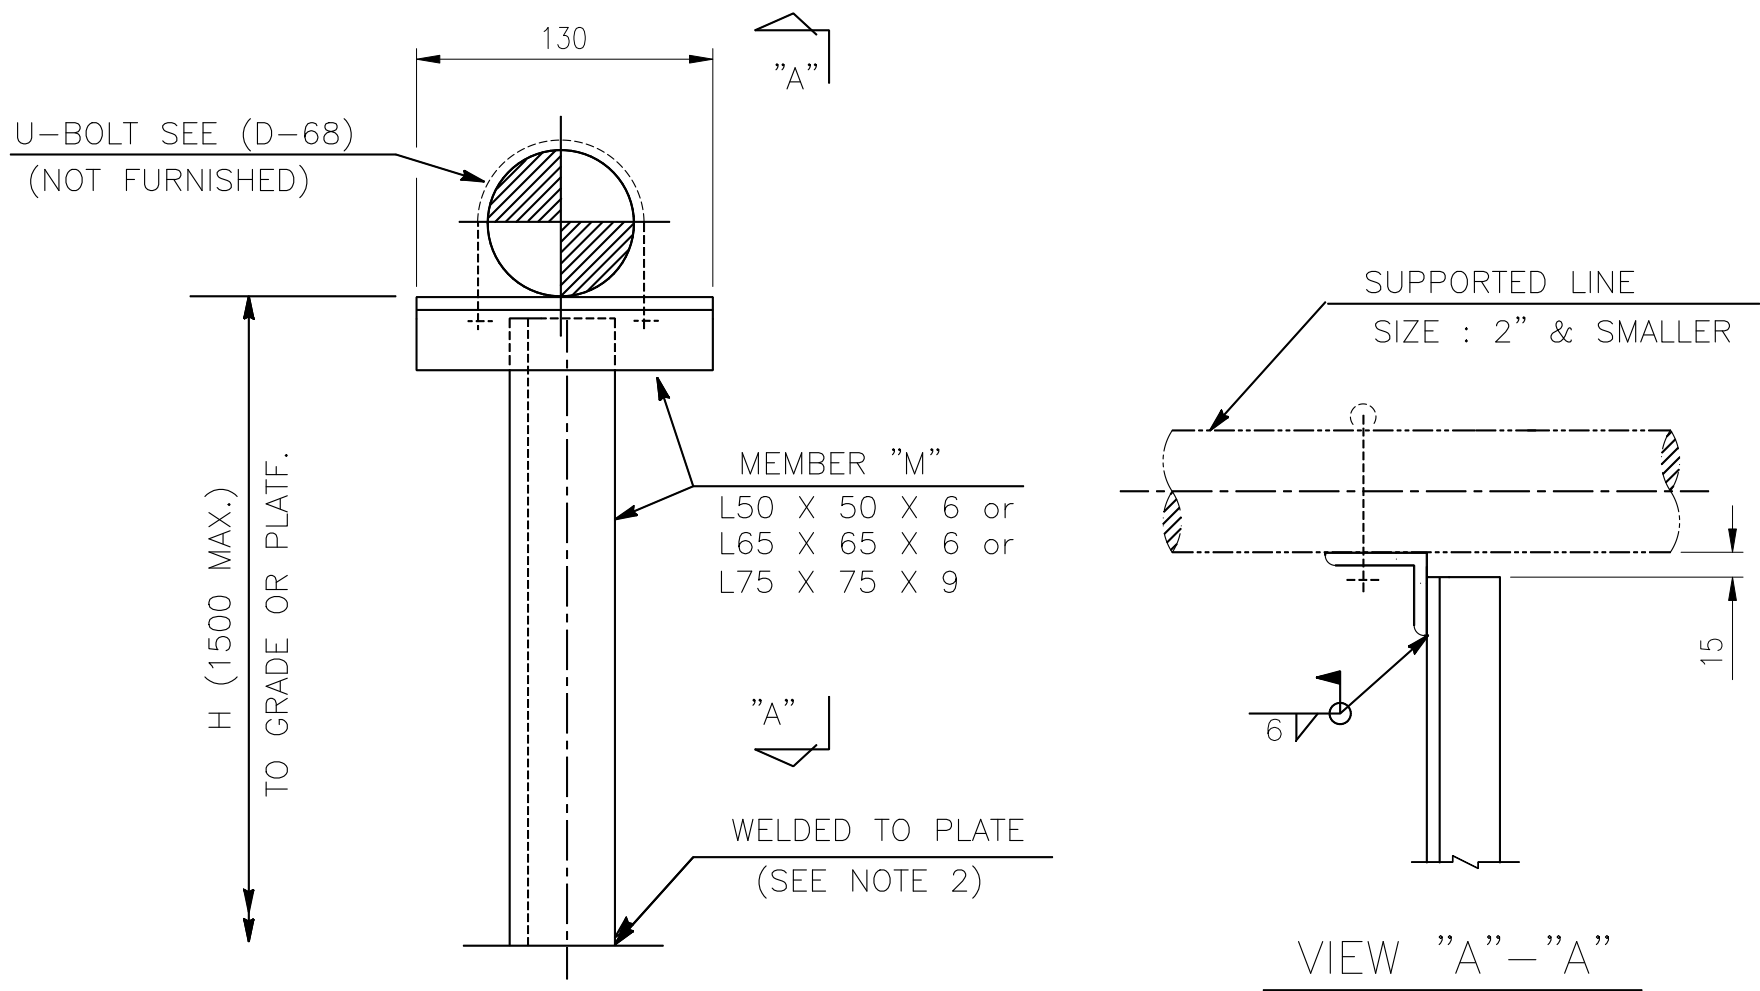

ELEV.

NOTES :

1. DIMENSION "H" SHALL BE CUT TO SUIT IN FIELD .
2. THIS TYPE SHALL BE USED WITH M-42 TO DETERMINE THE LOWER COMPONENT TYPE. IN THIS DETAIL, USE TYPE-D,L,P,&R ONLY.
3. DESIGNATION NUMBER DENOTE AS FOLLOWS :
05-L50-05L
DENOTE THE LOWER COMPONENT TYPE SEE M-42
DENOTE DIMENSION "H" (IN 100mm) (SEE NOTE 4)
DENOTE MEMBER "M"
DENOTE TYPE NO.
4. IF THE LOWER COMPONENT TYPE-L IS USED, DIMENSION "H" SHALL BE COUNTED FROM THE ELEVATION OF THE LOWEST POINT OF PAVING.

FILE: D-5M.DWG

中威工程顧問股份有限公司 CHUNG WEI ENGINEERING CONSULTING CO., LTD.						ENGINEERING STANDARD	
						HP6-DSD-A4-500-001	
BY	SHIH		CHK.	YANG		D-5	REV.
DATE	7/15/'24		APPR.	CHEN			1