


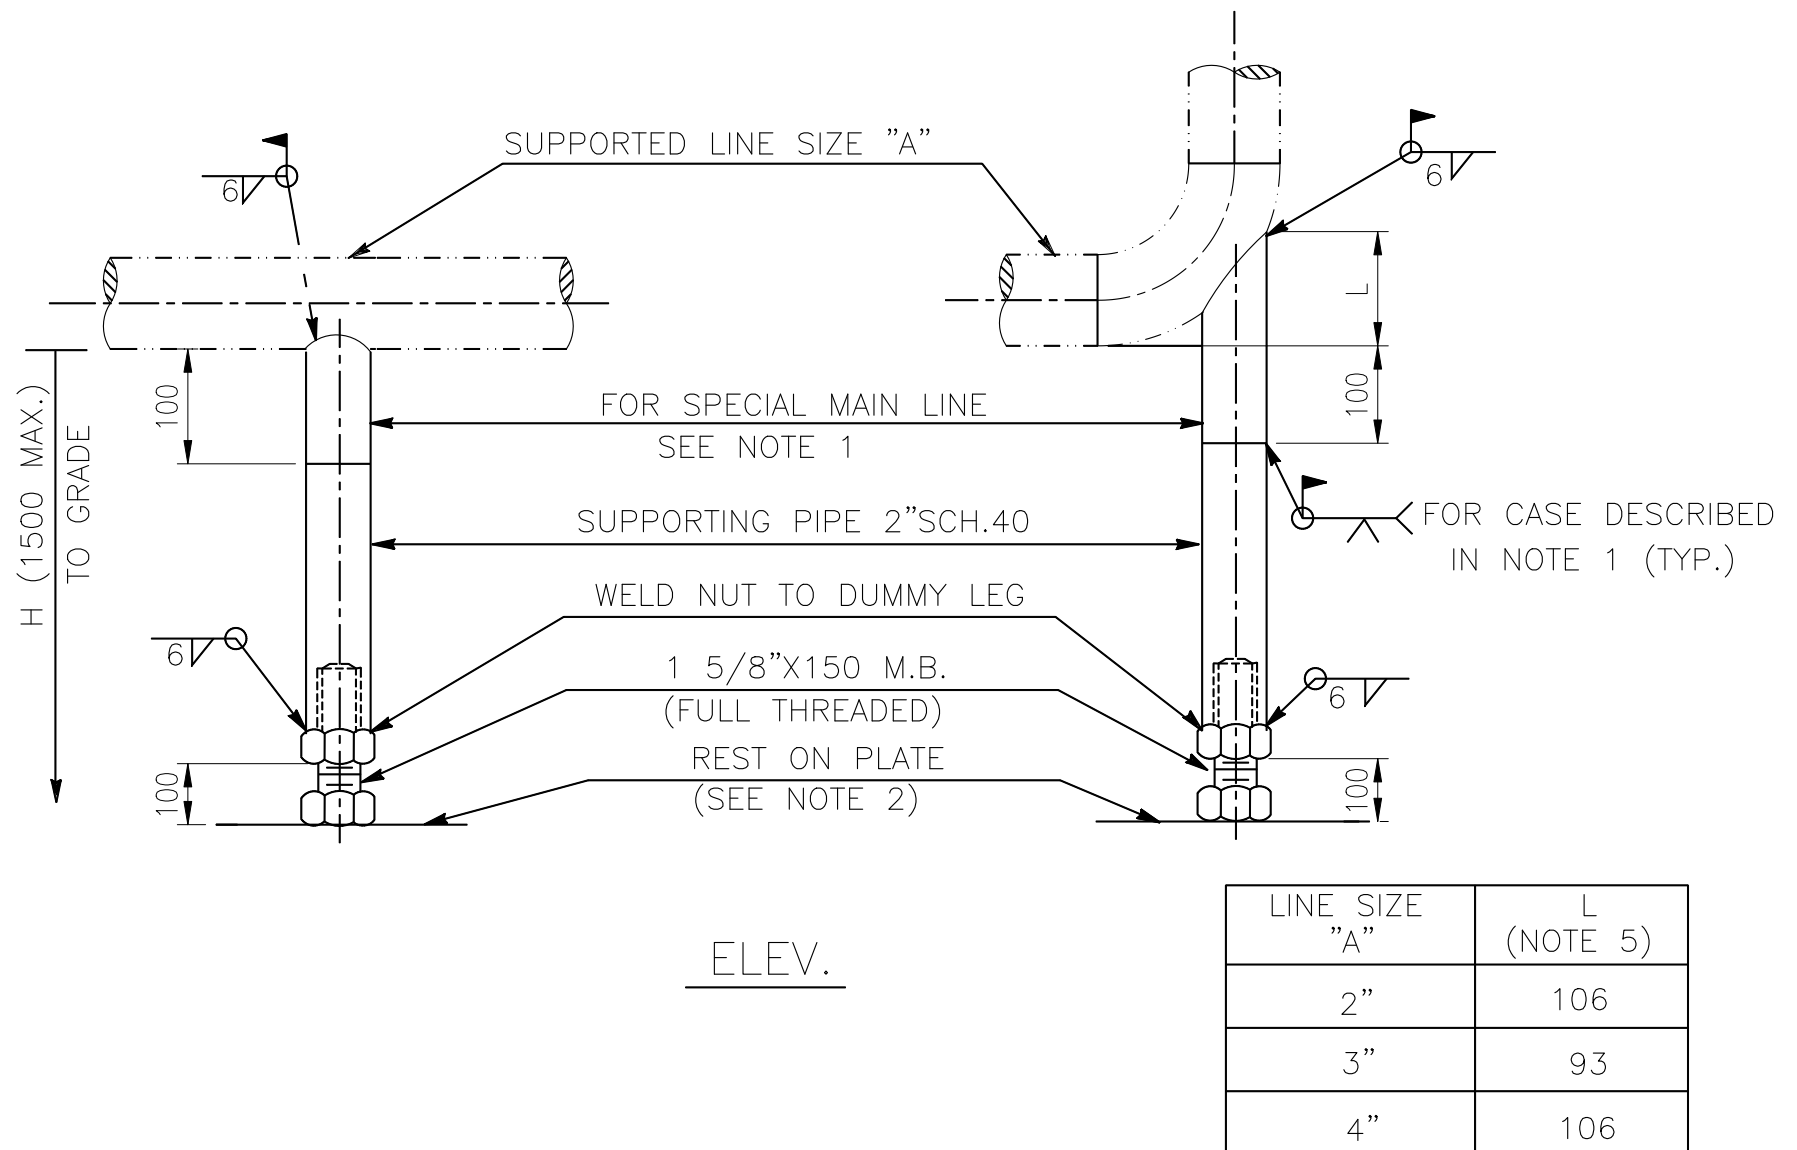

NOTES :

1. FOR ALLOY STEEL, STAINLESS STEEL & STRESS RELIEF LINES, THE MATERIALS SHALL BE THE SAME AS MAIN LINES.
2. THIS TYPE SHALL BE USED WITH M-42 TO DETERMINE THE LOWER COMPONENT TYPE. IN THIS DETAIL, USE TYPE-B & H ONLY.
3. DESIGNATION NUMBER DENOTE AS FOLLOWS :

09-2B-05B

DENOTE THE LOWER COMPONENT TYPE SEE M-42

DENOTE DIMENSION "H" (IN 100mm) (SEE NOTE 6)

DENOTE SUPPORTED LINE SIZE "A"

DENOTE TYPE NO.
4. DIMENSION "H" SHALL BE CUT TO SUIT IN FIELD .
5. DIMENSION "L" IS BASED ON LONG RADIUS ELBOW TO WHICH DUMMY PIPE IS WELDED.
6. IF THE LOWER COMPONENT TYPE-B IS USED, DIMENSION "H" SHALL BE COUNTED FROM THE ELEVATION OF THE LOWEST POINT OF PAVING.

中威工程顧問股份有限公司 CHUNG WEI ENGINEERING CONSULTING CO., LTD. DETAIL OF PIPE SUPPORT TYPE-09						ENGINEERING STANDARD	
						HP6-DSD-A4-500-001	
BY	SHIH		CHK.	YANG		D-9	REV. 1
DATE	7/15/'24		APPR.	CHEN			