


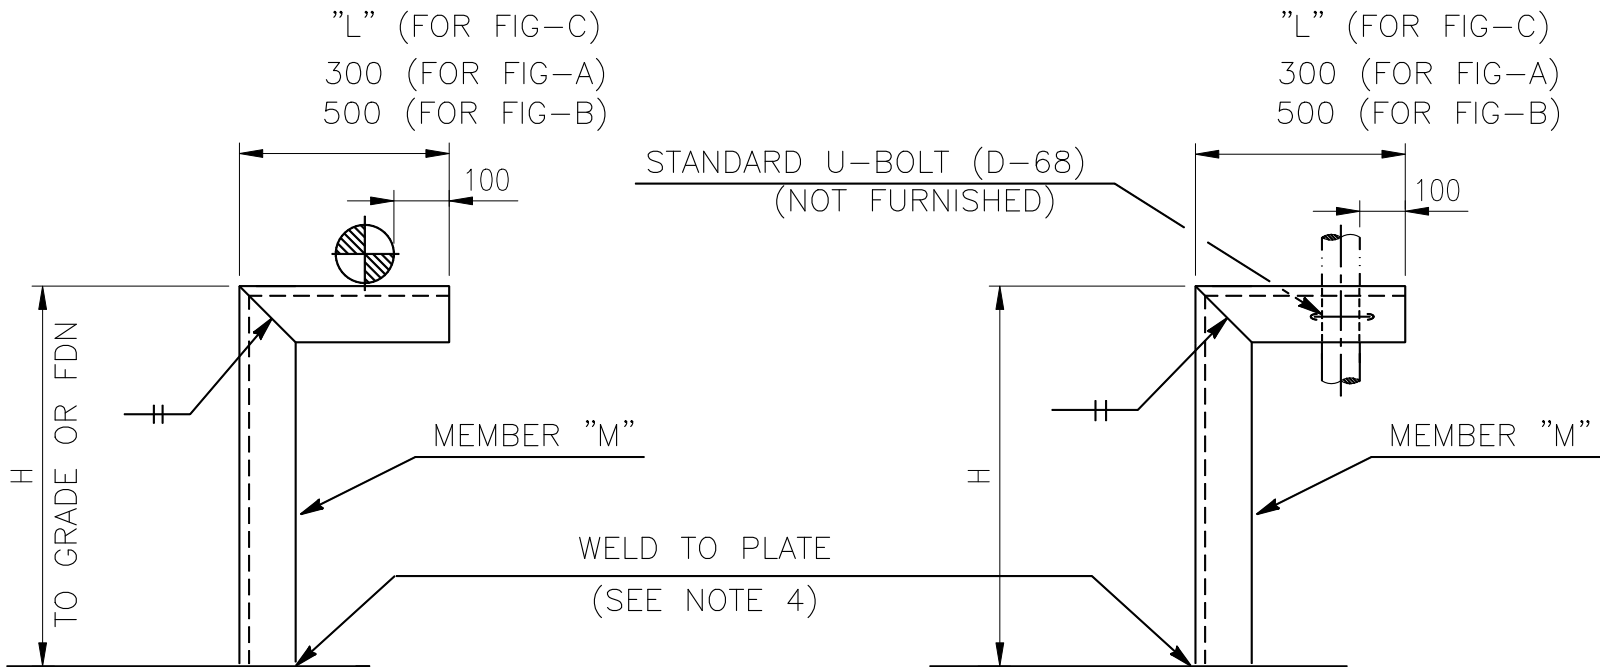


ELEV.

MEMBER "M"	H (MAX.)
L50X50X6	1000
L65X65X6	1000
L75X75X9	1500
C100X50X5	2000

NOTES :

1. DESIGNATION NUMBER DENOTE AS FOLLOWS :

22-L50-05(A)L-07

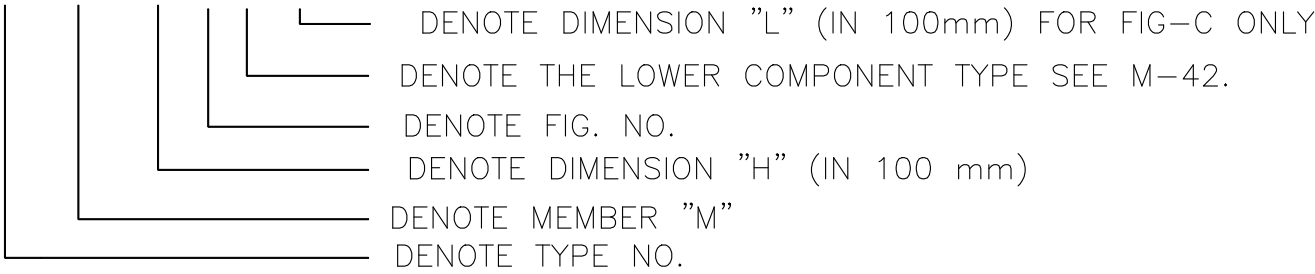

2. DIMENSION "H" SHALL BE CUT TO SUIT IN FIELD .

3. IF THE FOUNDATION IS NOT USED IN THIS DETAIL, DIMENSION "H" SHALL BE COUNTED FROM THE ELEVATION OF THE LOWEST POINT OF PAVING.

4. THIS TYPE SHALL BE USED WITH M-42 TO DETERMINE THE LOWER COMPONENT TYPE. IN THIS DETAIL, USE TYPE L & P ONLY.

FILE: D-24M.DWG

中威工程顧問股份有限公司 CHUNG WEI ENGINEERING CONSULTING CO., LTD.						ENGINEERING STANDARD	
						HP6-DSD-A4-500-001	
BY	SHIH		CHK.	YANG		D-24	
DATE	7/15/'24		APPR.	CHEN			
DETAIL OF PIPE SUPPORT TYPE-22						REV. 1	