

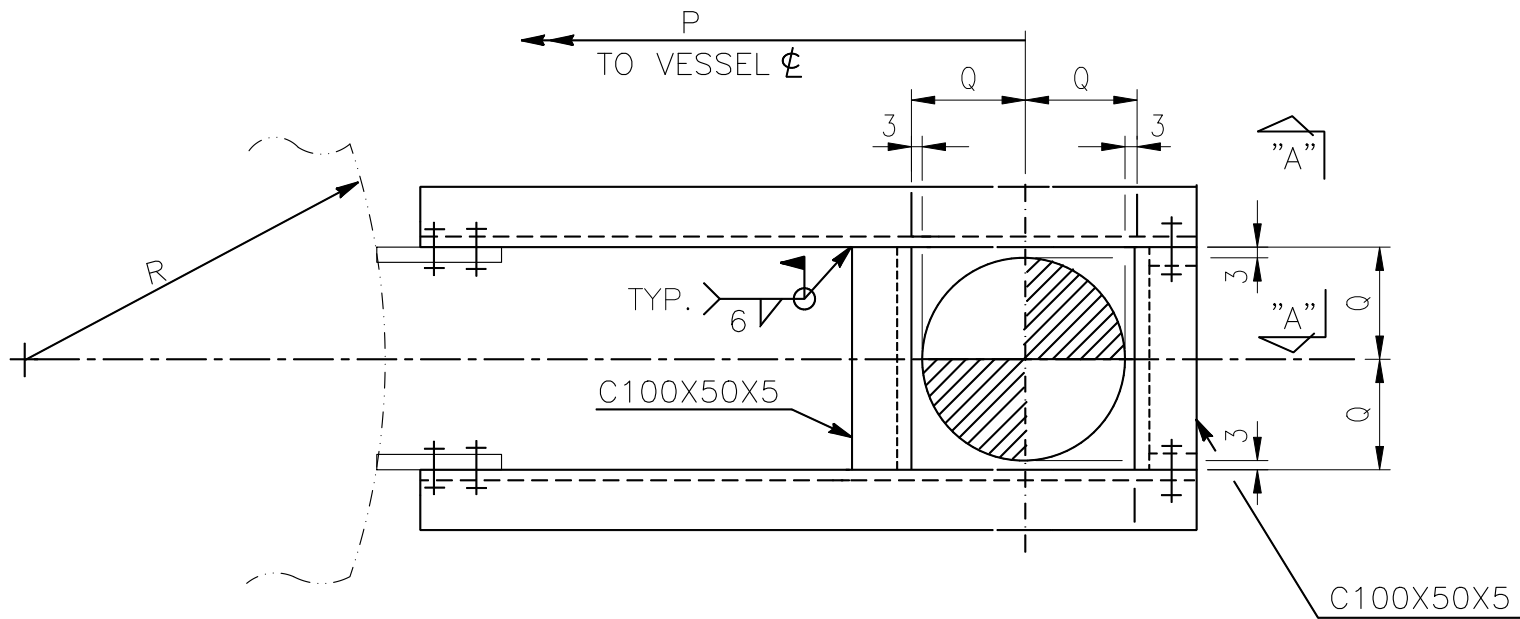


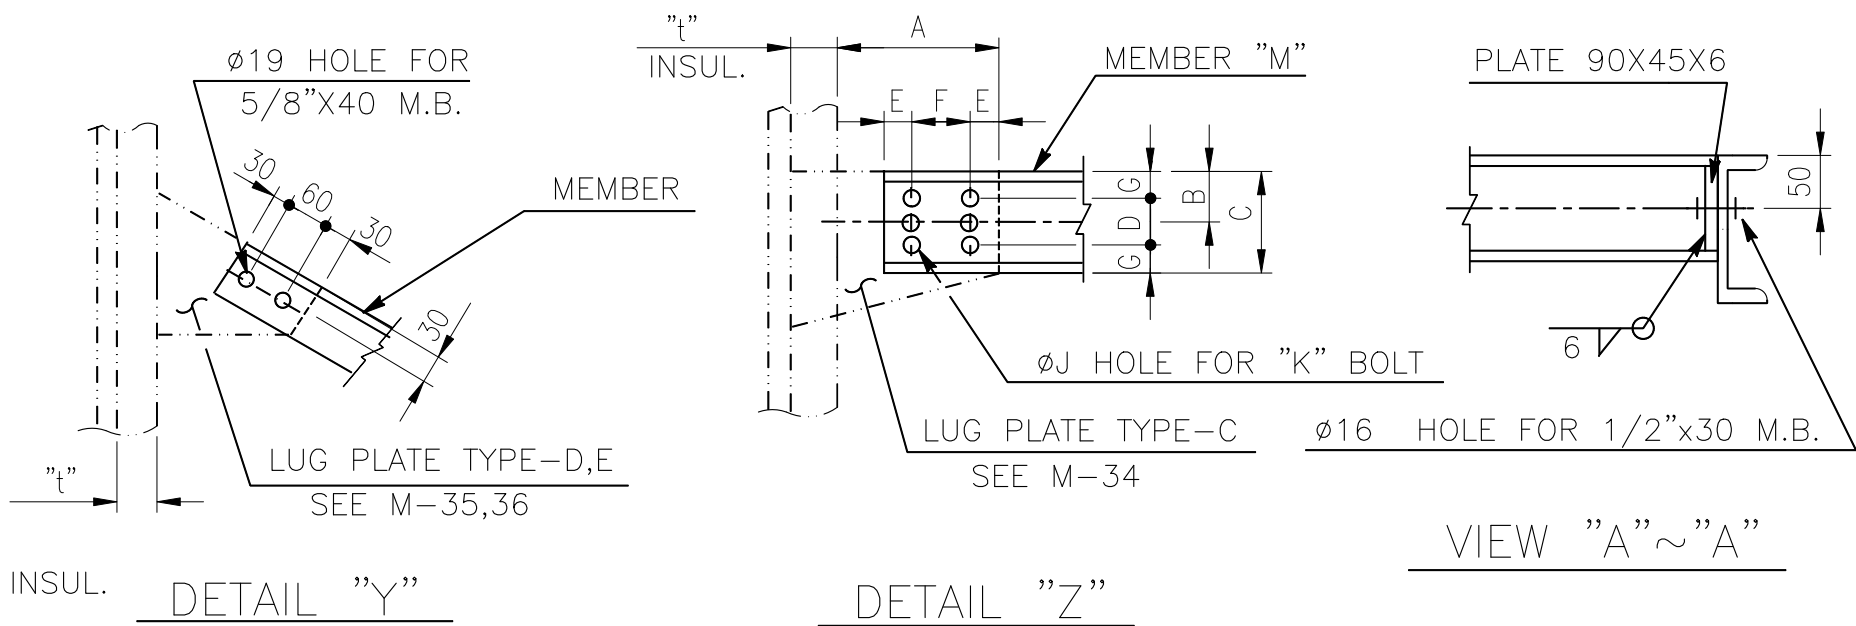

PLAN

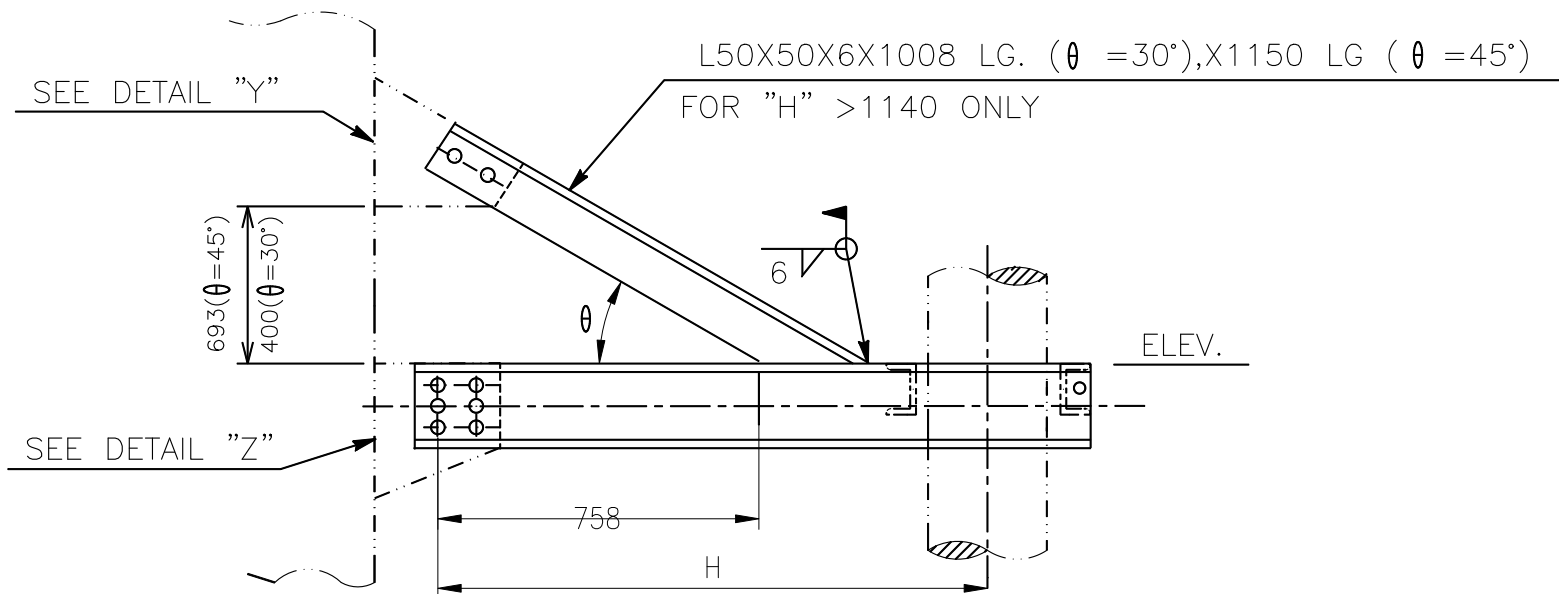

LINE SIZE	8"	10"	12"	14"
Q (mm)	113	140	165	181

FILE: D-54M.DWG

中威工程顧問股份有限公司 CHUNG WEI ENGINEERING CONSULTING CO., LTD.						DETAIL OF PIPE SUPPORT TYPE-45 (1 OF 2)		ENGINEERING STANDARD	
								HP6-DSD-A4-500-001	
BY	SHIH		CHK.	YANG				D-54	
DATE	7/15/'24		APPR.	CHEN					