


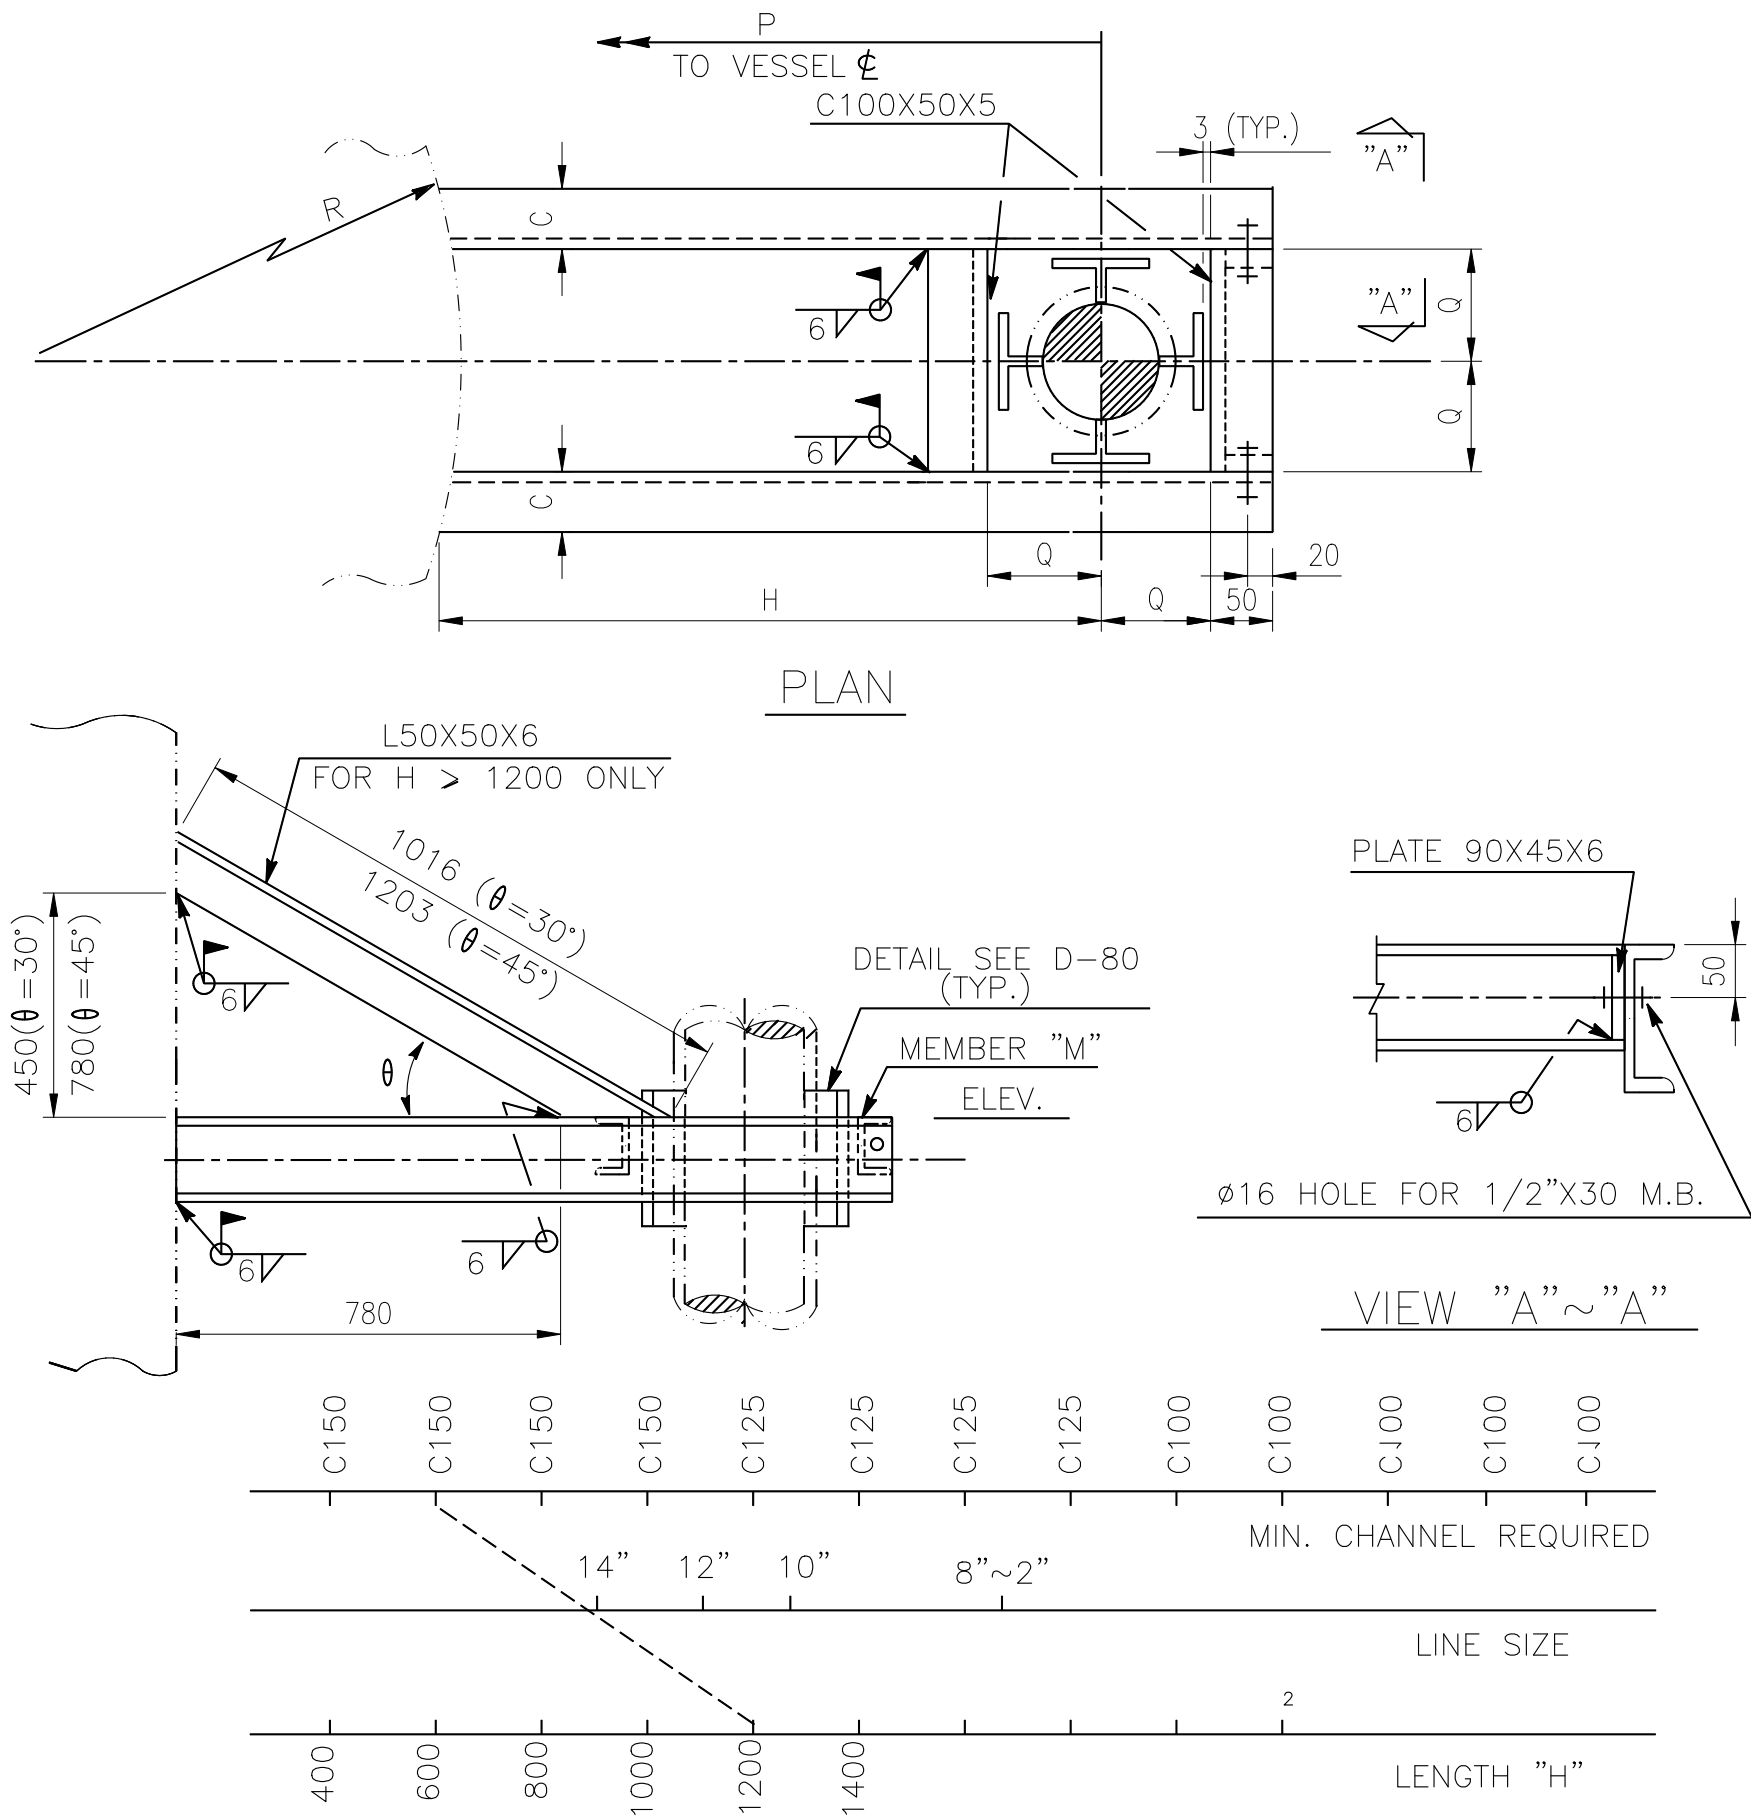

NOTES : 1. DESIGNATION NUMBER DENOTE AS FOLLOWS :

46-8B-C100-840 A OR B-175

DENOTE TYPE NO. DENOTE SUPPORTED LINE SIZE

MODIFY DIMENSION "Q" (IN mm) IF ANY

SEE NOTE 2 DENOTE LENGTH "H" (IN mm)

DENOTE MEMBER "M"

2. A: FOR $\theta = 30^\circ$, B: FOR $\theta = 45^\circ$

中威工程顧問股份有限公司
CHUNG WEI ENGINEERING CONSULTING CO., LTD.

DETAIL OF PIPE SUPPORT
TYPE-46

ENGINEERING STANDARD
HP6-DSD-A4-500-001
D-56 REV. 1

BY	SHIH		CHK.	YANG	
DATE	7/15/'24		APPR.	CHEN	