

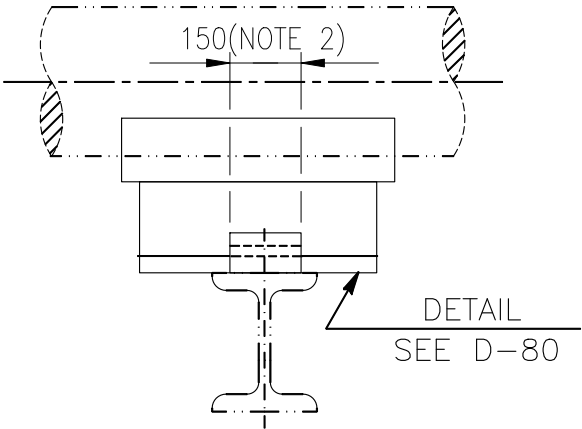
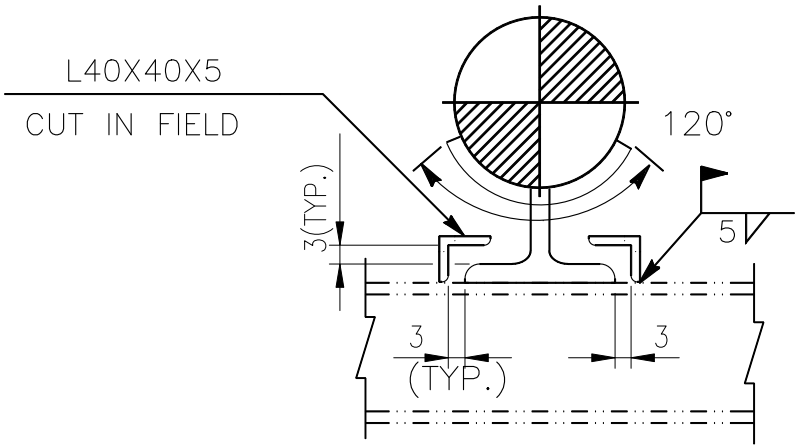


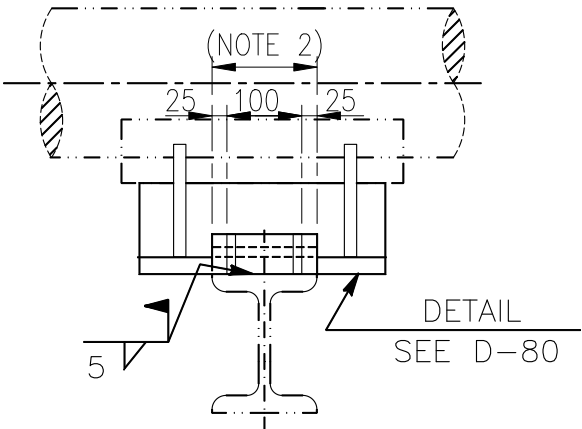

(8" & SMALLER)

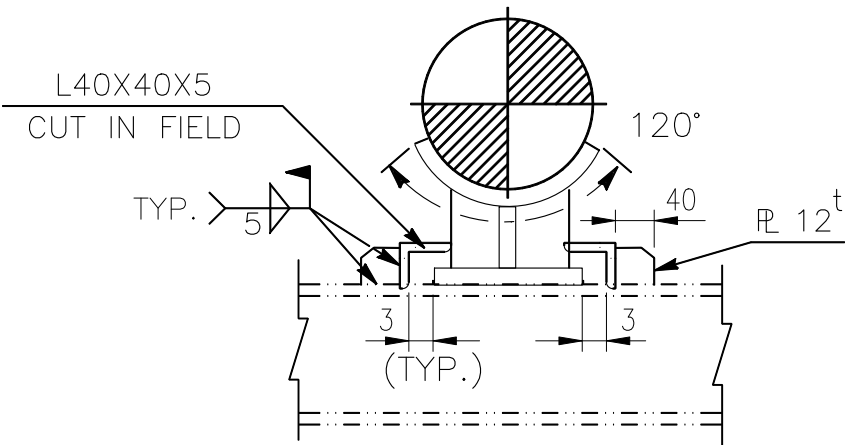


(10" TO 24")

ELEV.

NOTES :

1. DESIGNATION NUMBER DENOTE AS FOLLOWS :

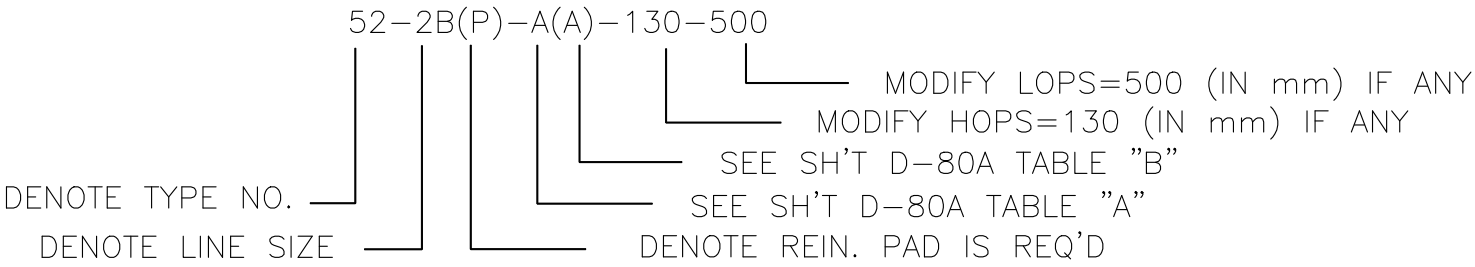

2. THE MAX. LENGTH OF THIS MEMBER SHALL NOT EXCEED THE WIDTH OF BEAM.

3. HOPS=HEIGHT OF PIPE SHOE
LOPS=LENGTH OF PIPE SHOE

FILE: D-63M.DWG

中威工程顧問股份有限公司 CHUNG WEI ENGINEERING CONSULTING CO., LTD.						ENGINEERING STANDARD	
						HP6-DSD-A4-500-001	
BY	SHIH		CHK.	YANG		DETAIL OF PIPE SUPPORT TYPE-52	REV.
DATE	7/15/'24		APPR.	CHEN			1