
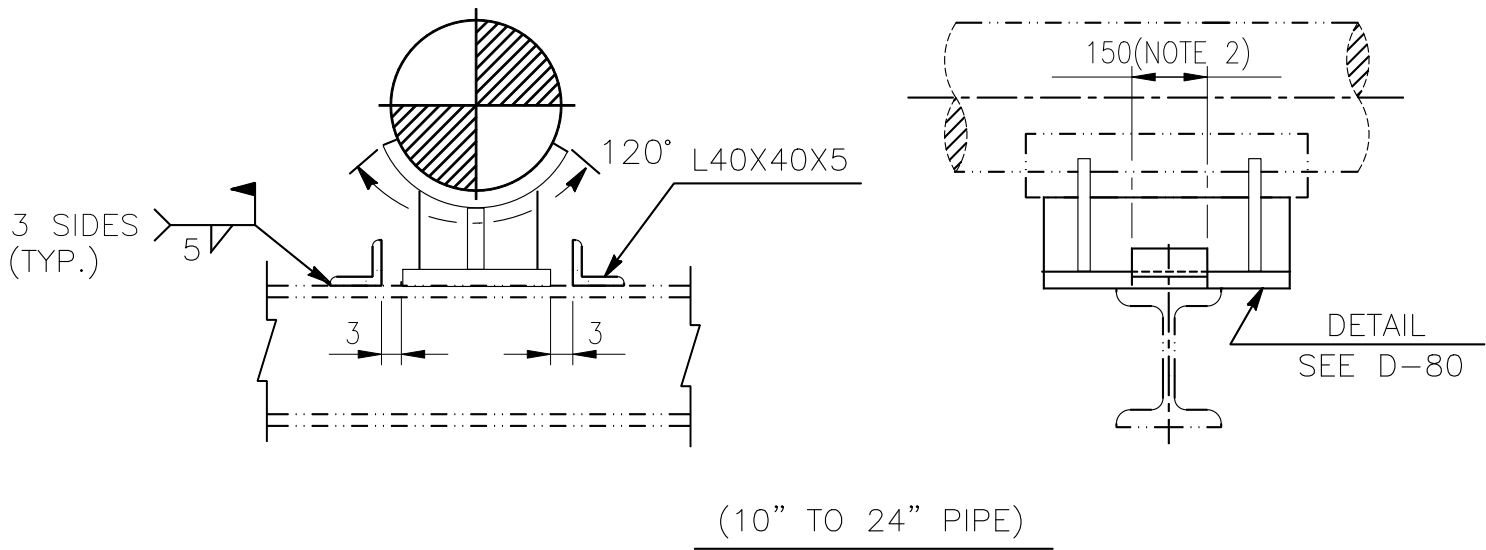



FOR PIPE SIZE 3/4"-24"

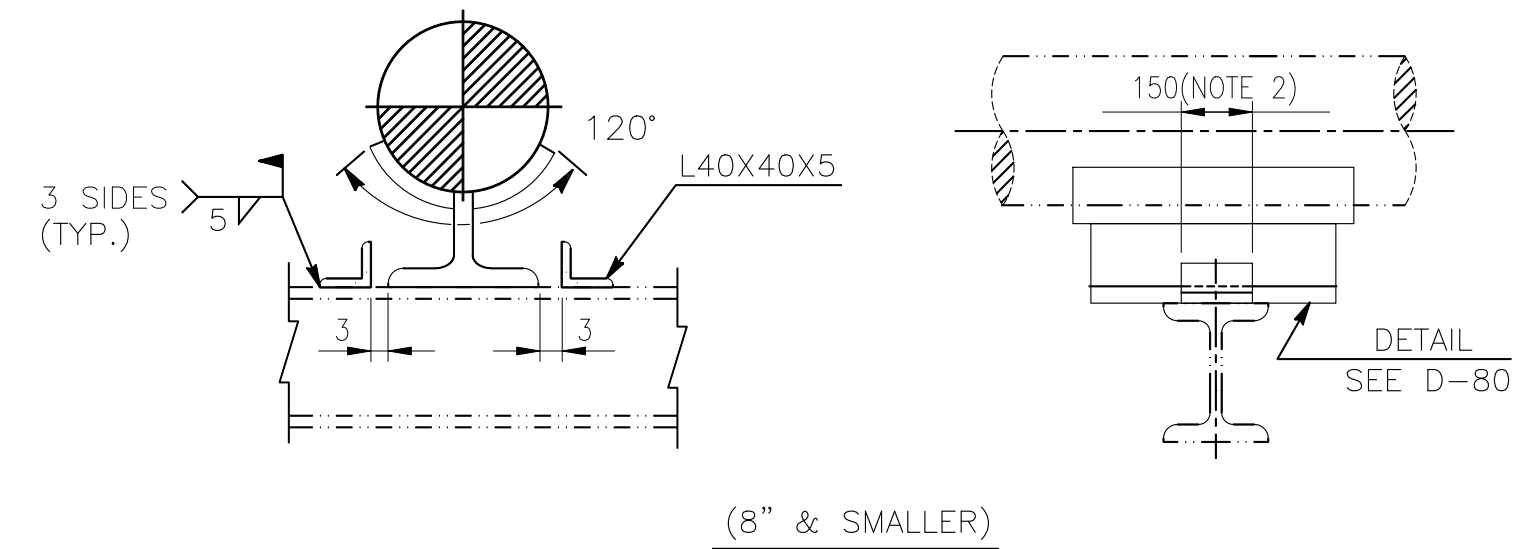

ELEV.

NOTES :

1. DESIGNATION NUMBER DENOTE AS FOLLOWS :

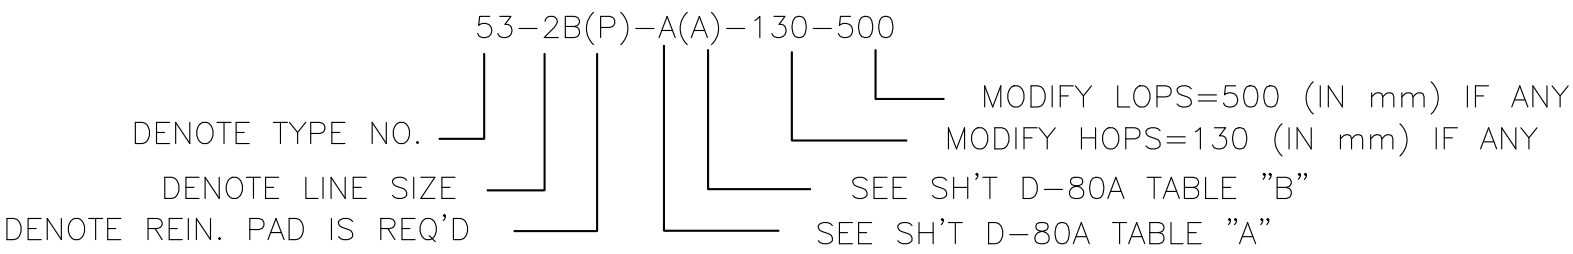

2. THE MAX. LENGTH OF THIS MEMBER SHALL NOT EXCEED THE WIDTH OF BEAM.

3. HOPS=HEIGHT OF PIPE SHOE, LOPS=LENGTH OF PIPE SHOE.

FILE: D-64M.DWG

|                                                            |          |  |       |      |  |                      |      |
|------------------------------------------------------------|----------|--|-------|------|--|----------------------|------|
| 中威工程顧問股份有限公司<br>CHUNG WEI ENGINEERING CONSULTING CO., LTD. |          |  |       |      |  | ENGINEERING STANDARD |      |
|                                                            |          |  |       |      |  | HP6-DSD-A4-500-001   |      |
| BY                                                         | SHIH     |  | CHK.  | YANG |  | D-64                 | REV. |
| DATE                                                       | 7/15/'24 |  | APPR. | CHEN |  |                      | 1    |

DETAIL OF PIPE SUPPORT  
TYPE-53

(1 OF 2)