


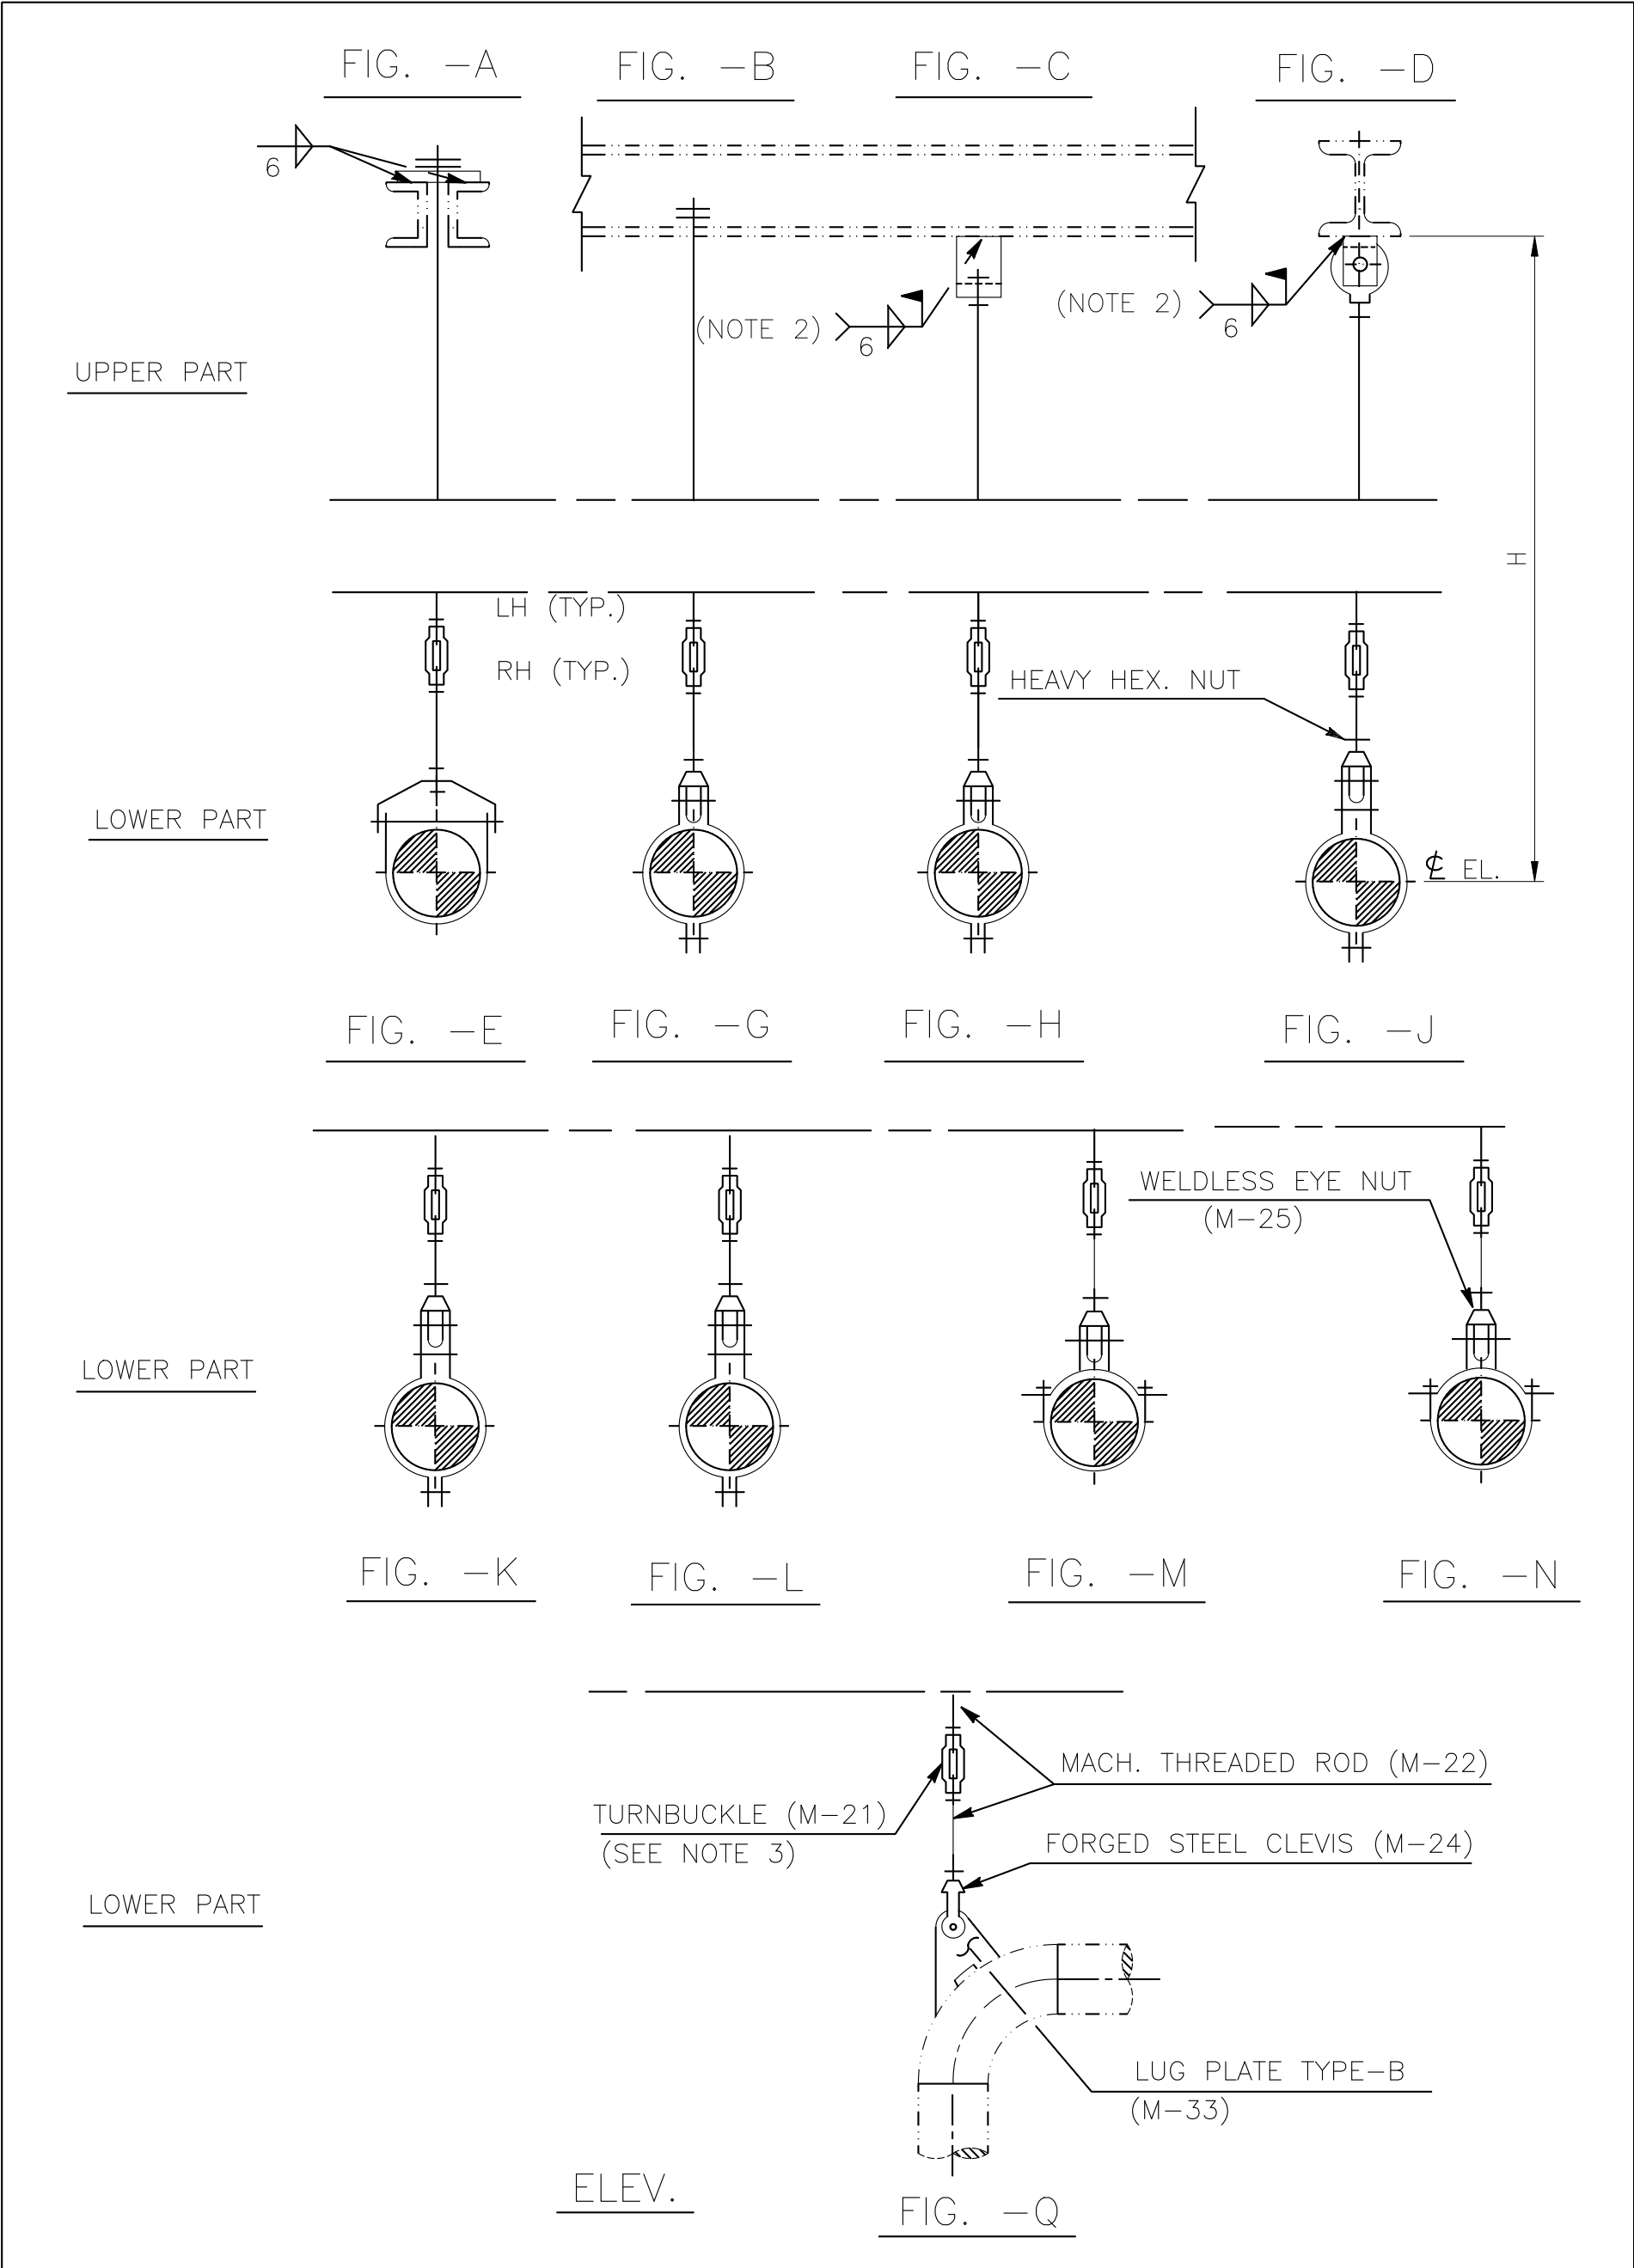

FILE: D-75M.DWG

中威工程顧問股份有限公司						ENGINEERING STANDARD	
CHUNG WEI ENGINEERING CONSULTING CO., LTD.						HP6-DSD-A4-500-001	
BY	SHIH		CHK.	YANG		D-75	REV. 1
DATE	7/15/'24		APPR.	CHEN			

DETAIL OF PIPE SUPPORT
TYPE-62